

ASPEN

DRAWING INDEX

- 0.0 COVER SHEET
- 2.0 SLAB AND TERRACE FLOOR PLAN
- 2.1 FIRST FLOOR PLAN
- 2.1.1 FLOOR PLAN OPTIONS
- 3.11 ELEVATION "11" FRONT & REAR
- 3.12 ELEVATION "11" SIDES & ROOF PLAN
- 5.0 TERRACE FLOOR ELECTRICAL PLAN
- 5.1 FIRST & SECOND FLOOR ELECTRICAL PLAN
- 5.1.1 ELECTRICAL OPTIONS

BUILDING INFO.

DESIGN CODES

INTERNATIONAL RESIDENTIAL CODE 2018 EDITION – WITH ALL GEORGIA AMENDMENTS
INTERNATIONAL FIRE CODE 2018 EDITION – WITH ALL GEORGIA AMENDMENTS
INTERNATIONAL PLUMBING CODE 2018 EDITION – WITH ALL GEORGIA AMENDMENTS
INTERNATIONAL MECHANICAL CODE 2018 EDITION – WITH ALL GEORGIA AMENDMENTS
INTERNATIONAL FUEL GAS CODE 2018 EDITION – WITH ALL GEORGIA AMENDMENTS
NATIONAL ELECTRICAL CODE 2023 EDITION
INTERNATIONAL ENERGY CONSERVATION CODE 2018 EDITION – WITH ALL GEORGIA AMENDMENTS
2018 LIFE SAFETY CODE W/ GEORGIA AMENDMENTS

BUILDING CODE ANALYSIS

USE GROUP : ONE & TWO FAMILY DWELLING

CONSTRUCTION CLASS : UNPROTECTED

HEIGHT & AREA LIMITATION : 3 STORY MAXIMUM HGT 35 FEET

EMERGENCY ESCAPE : EGRESS OR RESCUE WINDOWS FROM SLEEPING ROOMS
SHALL HAVE MINIMUM OF 5.7 SQ. FT.

GARAGE/HOUSE CEILING/HOUSE ASSEMBLY :

DESIGN LOADS : LIVE LOAD:
SLEEPING = 30 PSF
NON-SLEEPING = 40 PSF
DECKS = 40 PSF
DEAD LOAD = 10 PSF
BASIC WIND SPEED = PER ENGINEERING
STAIR LOADS = 40 PSF
ROOF LIVE LOAD = 20 PSF
LATERAL SOIL PRESSURE = 30 PSF (ASSUMED)




PRODUCT ACTION REQUEST / REVISION TRACKING

SQUARE FOOTAGES

BASE PLAN	
TERRACE FLOOR	433 SQ. FT.
FIRST FLOOR	805 SQ. FT.
SECOND FLOOR	733 SQ. FT.
TOTAL HEATED AREA	1971 SQ. FT.
GARAGE	372 SQ. FT.
COVERED DECK	128 SQ. FT.
WIDTH / DEPTH	24'-0" x 34'-0"

5400 LAUREL SPRINGS PKWY,
BLDG 700, STE 702
SUWANEE GA 30024
770-789-7044

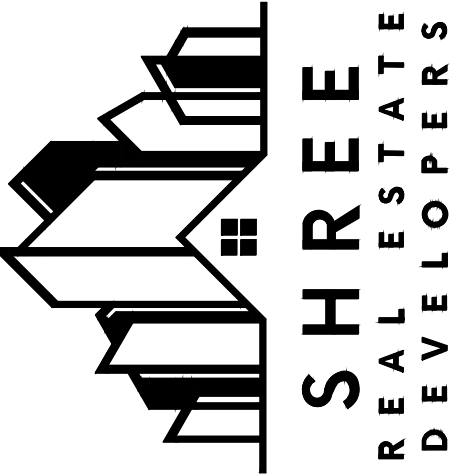

REVISIONS

No.	DESCRIPTION	No.	DESCRIPTION
1		6	
2		7	
3		8	
4		9	
5		10	

RELEASE FOR
CONSTRUCTION

PROJECT:
COVER PAGE
ASPEN

SHEET TITLE:
COVER PAGE

DESIGNED BY :	PLAN NAME:
DRAWN BY :	SCALE: 1/8"=1'-0"
CHECKED BY :	PRODUCT TYPE:
REVIEWED BY :	SHEET: 00
RELEASE DATE:	

GENERAL NOTES:

- G1CONSTRUCTION SHALL CONFORM WITH ALL APPLICABLE LOCAL CODES AND ORDINANCES
- G2ALL WALLS ARE FRAMED W/ 2X4 STUDS U.N.O W/ EXTERIOR & LOAD BEARING WALLS @ 16" O.C. INTERIOR NON-LOAD BEARING WALLS @ 24" O.C.
LOAD BEARING WALLS SYMBOL
████████
- G3BALLOON FRAME ALL TWO STORY WALLS. PROVIDE WOOD BLOCKING BEHIND CEILING FANS
- G4PROVIDE ADEQUATE BLOCKING FOR ALL WALL CABINETS.
- G5CLOSETS TO HAVE 1 ROD AND 1 SHELF WHERE SHOWN UNLESS NOTED OTHERWISE
- G61R&1S - SHELF 69" A.F.F. 2R&1S-SHELF & 80" A.F.F. 2nd ROD 38" A.F.F.
- G7LINEN CLOSETS AND PANTRIES TO HAVE (5) 16" DEEP SHELVES UNLESS NOTED OTHERWISE. FIRST SHELF TO BE @ 36" AFF W/ SHELF SPACING 12" O.C. ABV.
- G8UTILITY ROOM TO HAVE (1) 16" SHELF AT 60" A.F.F. ABOVE WASHER & DRYER. CABINETS ARE PER COMMUNITY SPECS.
- G9DOOR INTO THE HOUSE FROM THE GARAGE TO BE WEATHERSTRIPPED SOLID CORE
- G10ALL MIRROR WIDTHS TO BE 3" LESS THAN OVERALL VANITY WIDTH. MIRROR HEIGHTS ARE PER COMMUNITY SPECS
- G11CENTER OF TOILET TO BE A MIN. OF 15" FROM THE VERTICAL SURFACE OF SIDE WALLS, CABINETS OR OTHER OBSTRUCTION. PROVIDE A MIN OF 21" CLEAR FROM TOILET TO THE VERTICAL FACE OF A TUB OR OTHER OBSTRUCTION. EDGE OF TOILET TO BE A MIN. FO 4" FROM PEDESTAL OR WALL MOUNTED LAV.
- G12FACE EDGE OF SHOWER UNITS TO HAVE A MIN. 24" CLEAR TO ANY VERTICAL SURFACE.
- G13A/C PADS ARE TO BE 36"x36" OR 36"x72" FOR 2-UNIT A/C PAD
- G14STUB GAS LINE 6" AFF AT CENTERLINE OF RANGE
- G15FIRE CAULK ALL PLATE PENETRATIONS

FIREPLACE ROUGH OPENING

FP ROUGH OPENING SCHEDULE		
FP BOX SIZE:	OPNG WIDTH:	OPNG HEIGHT:
36" BOX	42"	34 5/8"
42" BOX	48"	34 5/8"

HEADERS

HEADER SCHEDULE		
SPAN:	FRAMING:	LABEL:
UP TO 6'-6"	2-2x12	HDR-A
6'-7" TO 9'-0"	2-9 1/4" LVL	HDR-B
OVER 9'-0"	BY ENGINEER	ENG.

- H1HEADER MATERIAL TO BE A MIN. # 2 S.Y.P.
- H2PROVIDE 2-2x12 HEADERS AT ALL GARAGE DOOR OPENINGS AND WINDOWS 6'-0" OR GREATER. HEADERS, LONGER THAN 9'-0", IF NOT SPECIFIED ON PLANS, ARE TO BE DESIGNED BY A REGISTERED PROFESSIONAL ENGINEER.
- H3LOCATE HEADER DIRECTLY ABOVE OPENING. PROVIDE CRIPPLE FRAMING FROM TOP PLATES TO HEADER AS REQUIRED.
- H4TABLE APPLIES TO ALL EXTERIOR WALLS AND LOAD BEARING INTERIOR WALLS. FOR NON-LOAD BEARING INTERIOR WALLS, USE 2-2x4'S CUT FROM STUDS.
- H5DO NOT USE TABLE IF HEADERS SUPPORT CONCENTRATED LOADS.

DRAINAGE



- D1PROVIDE SITE DRAINAGE AS REQUIRE BY SITE TOPOGRAPHY
- D2FINISH FLOOR SHALL BE A MIN. OF 8" ABOVE ADJ. FINISH GRADE FINISH GRADE SHALL SLOPE 5% FOR A MIN. DISTANCE OF 10'-0" FROM HOUSE TO AN APPROVED DRAINAGE SYS.

FLOORING ABBREVIATIONS

OPT ✱ WRF = FLOORING CHANGE LINE
WRF = WATER RESISTANT FLOORING
CPT = CARPET

PLUMBING

PLUMBING FIXTURES WILL NOT PENETRATE FIREWALLS UNDER ANY CIRCUMSTANCE

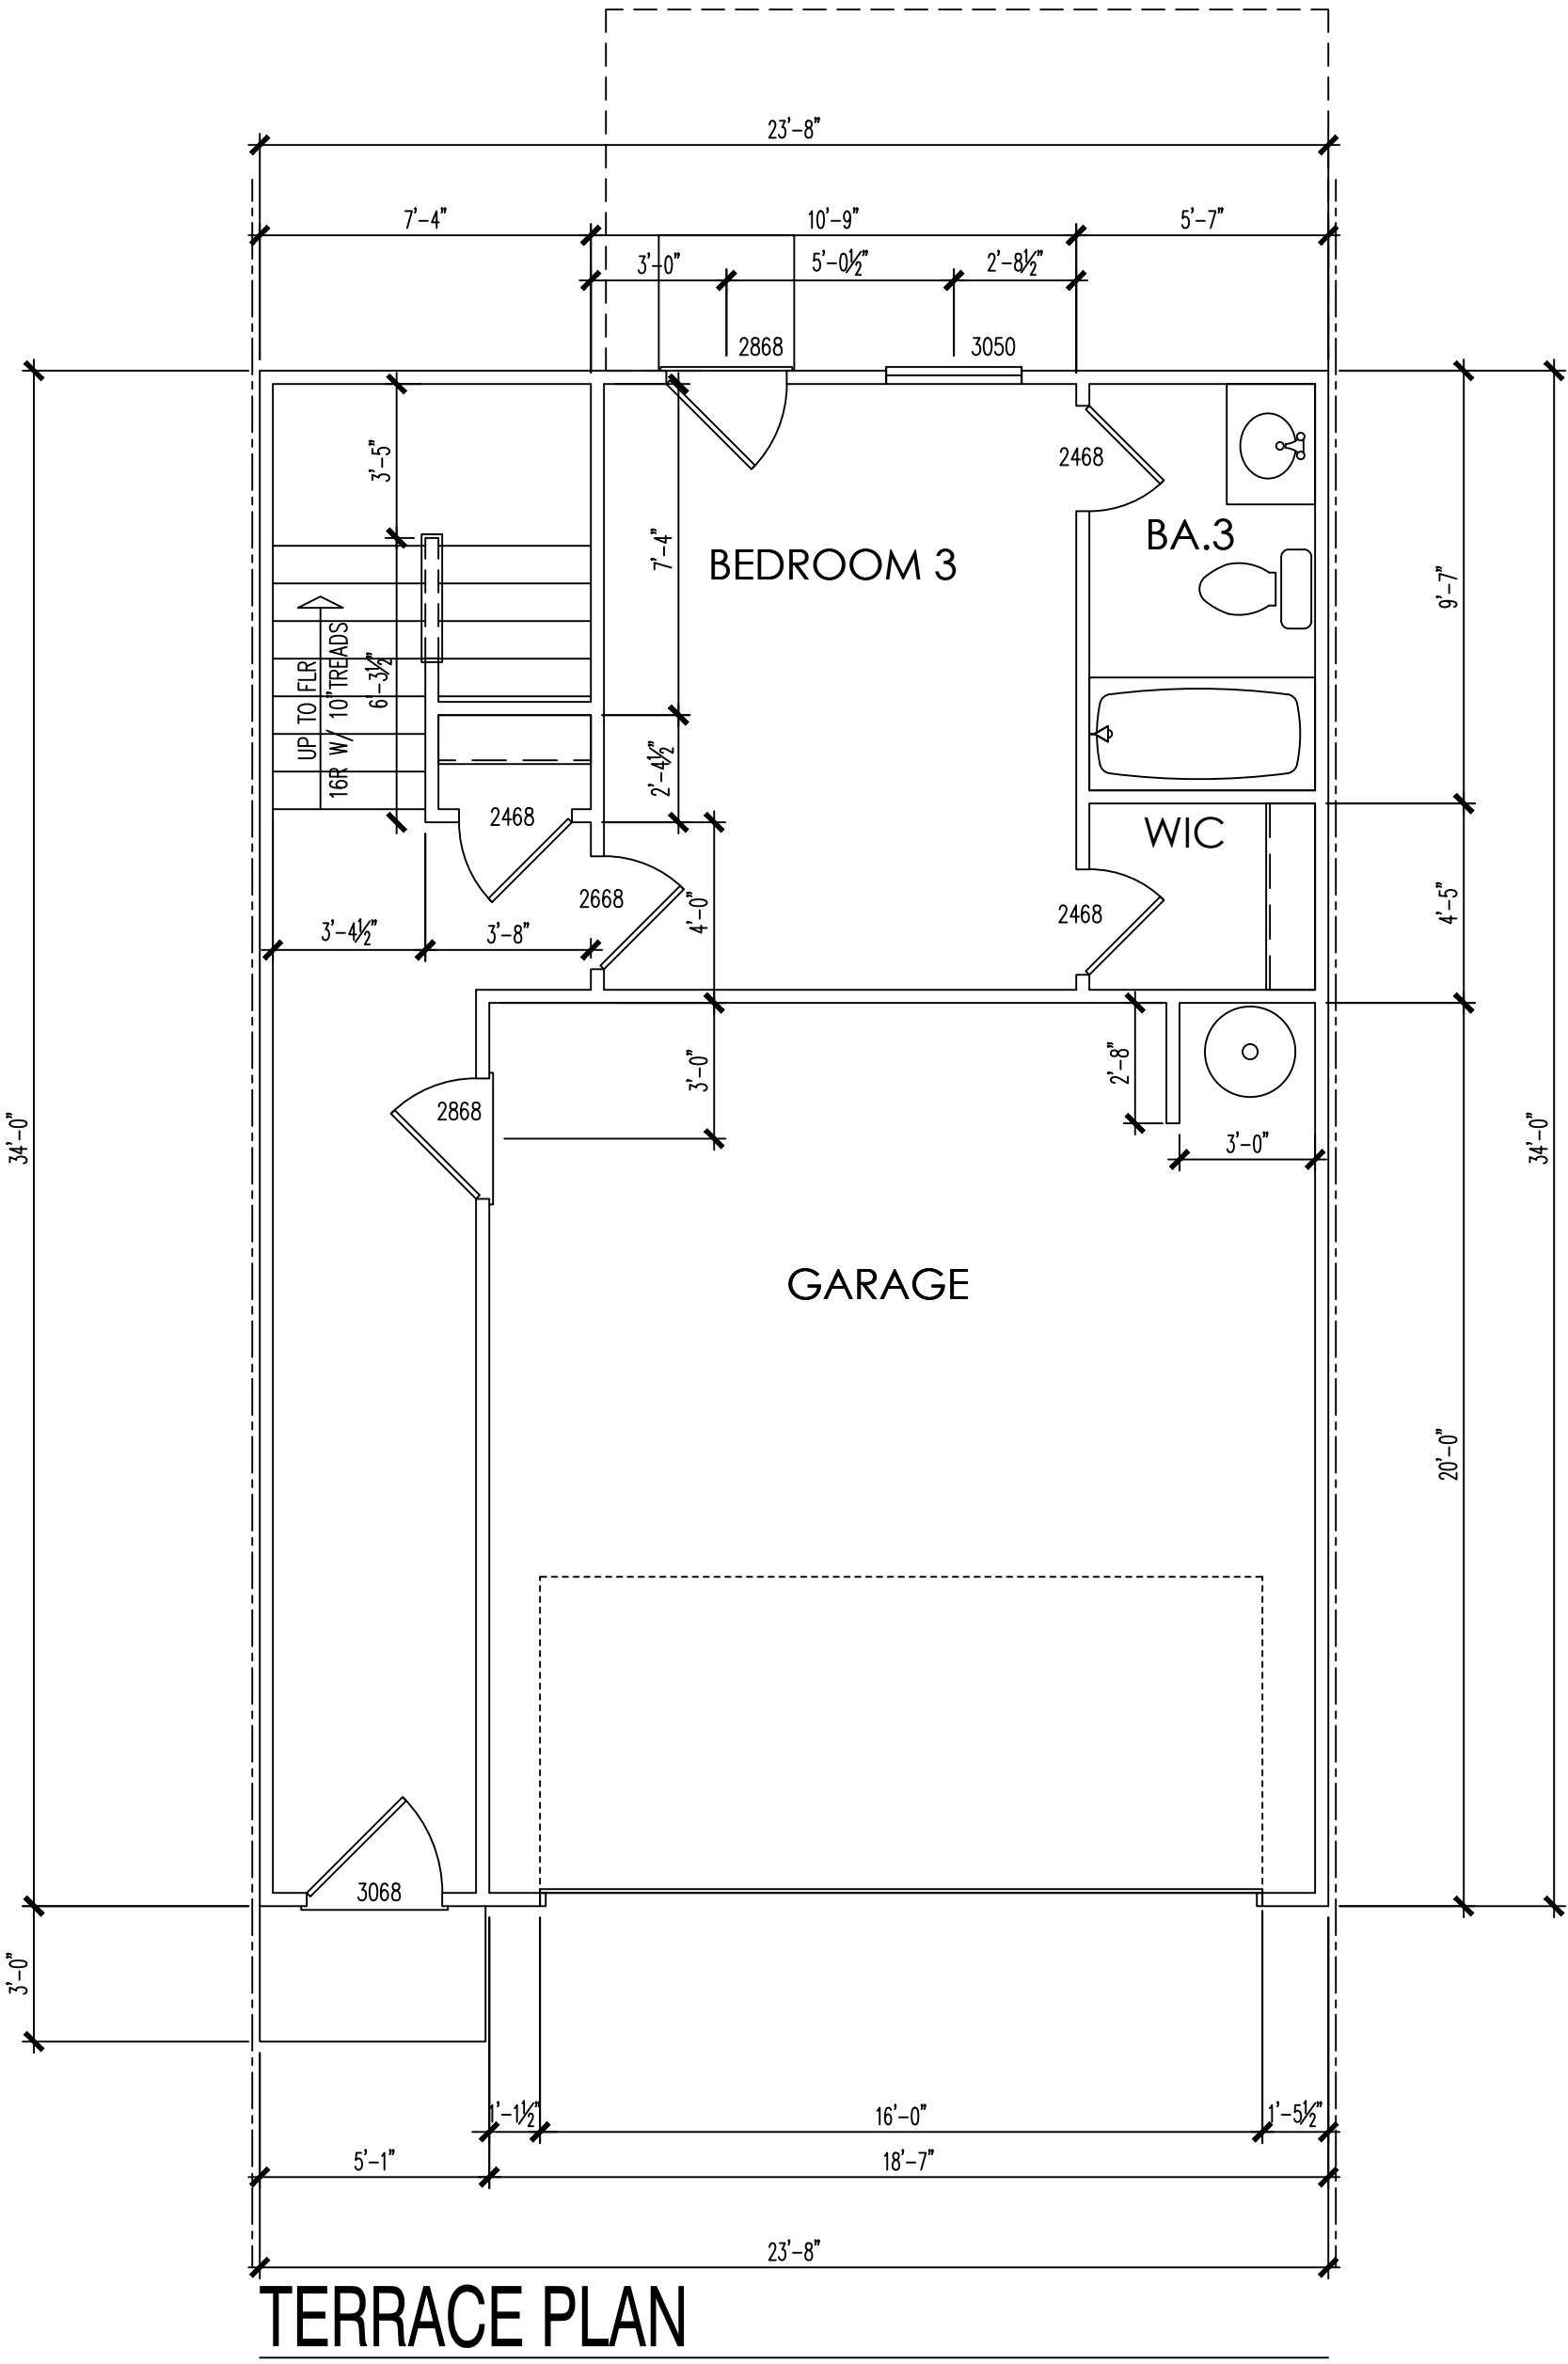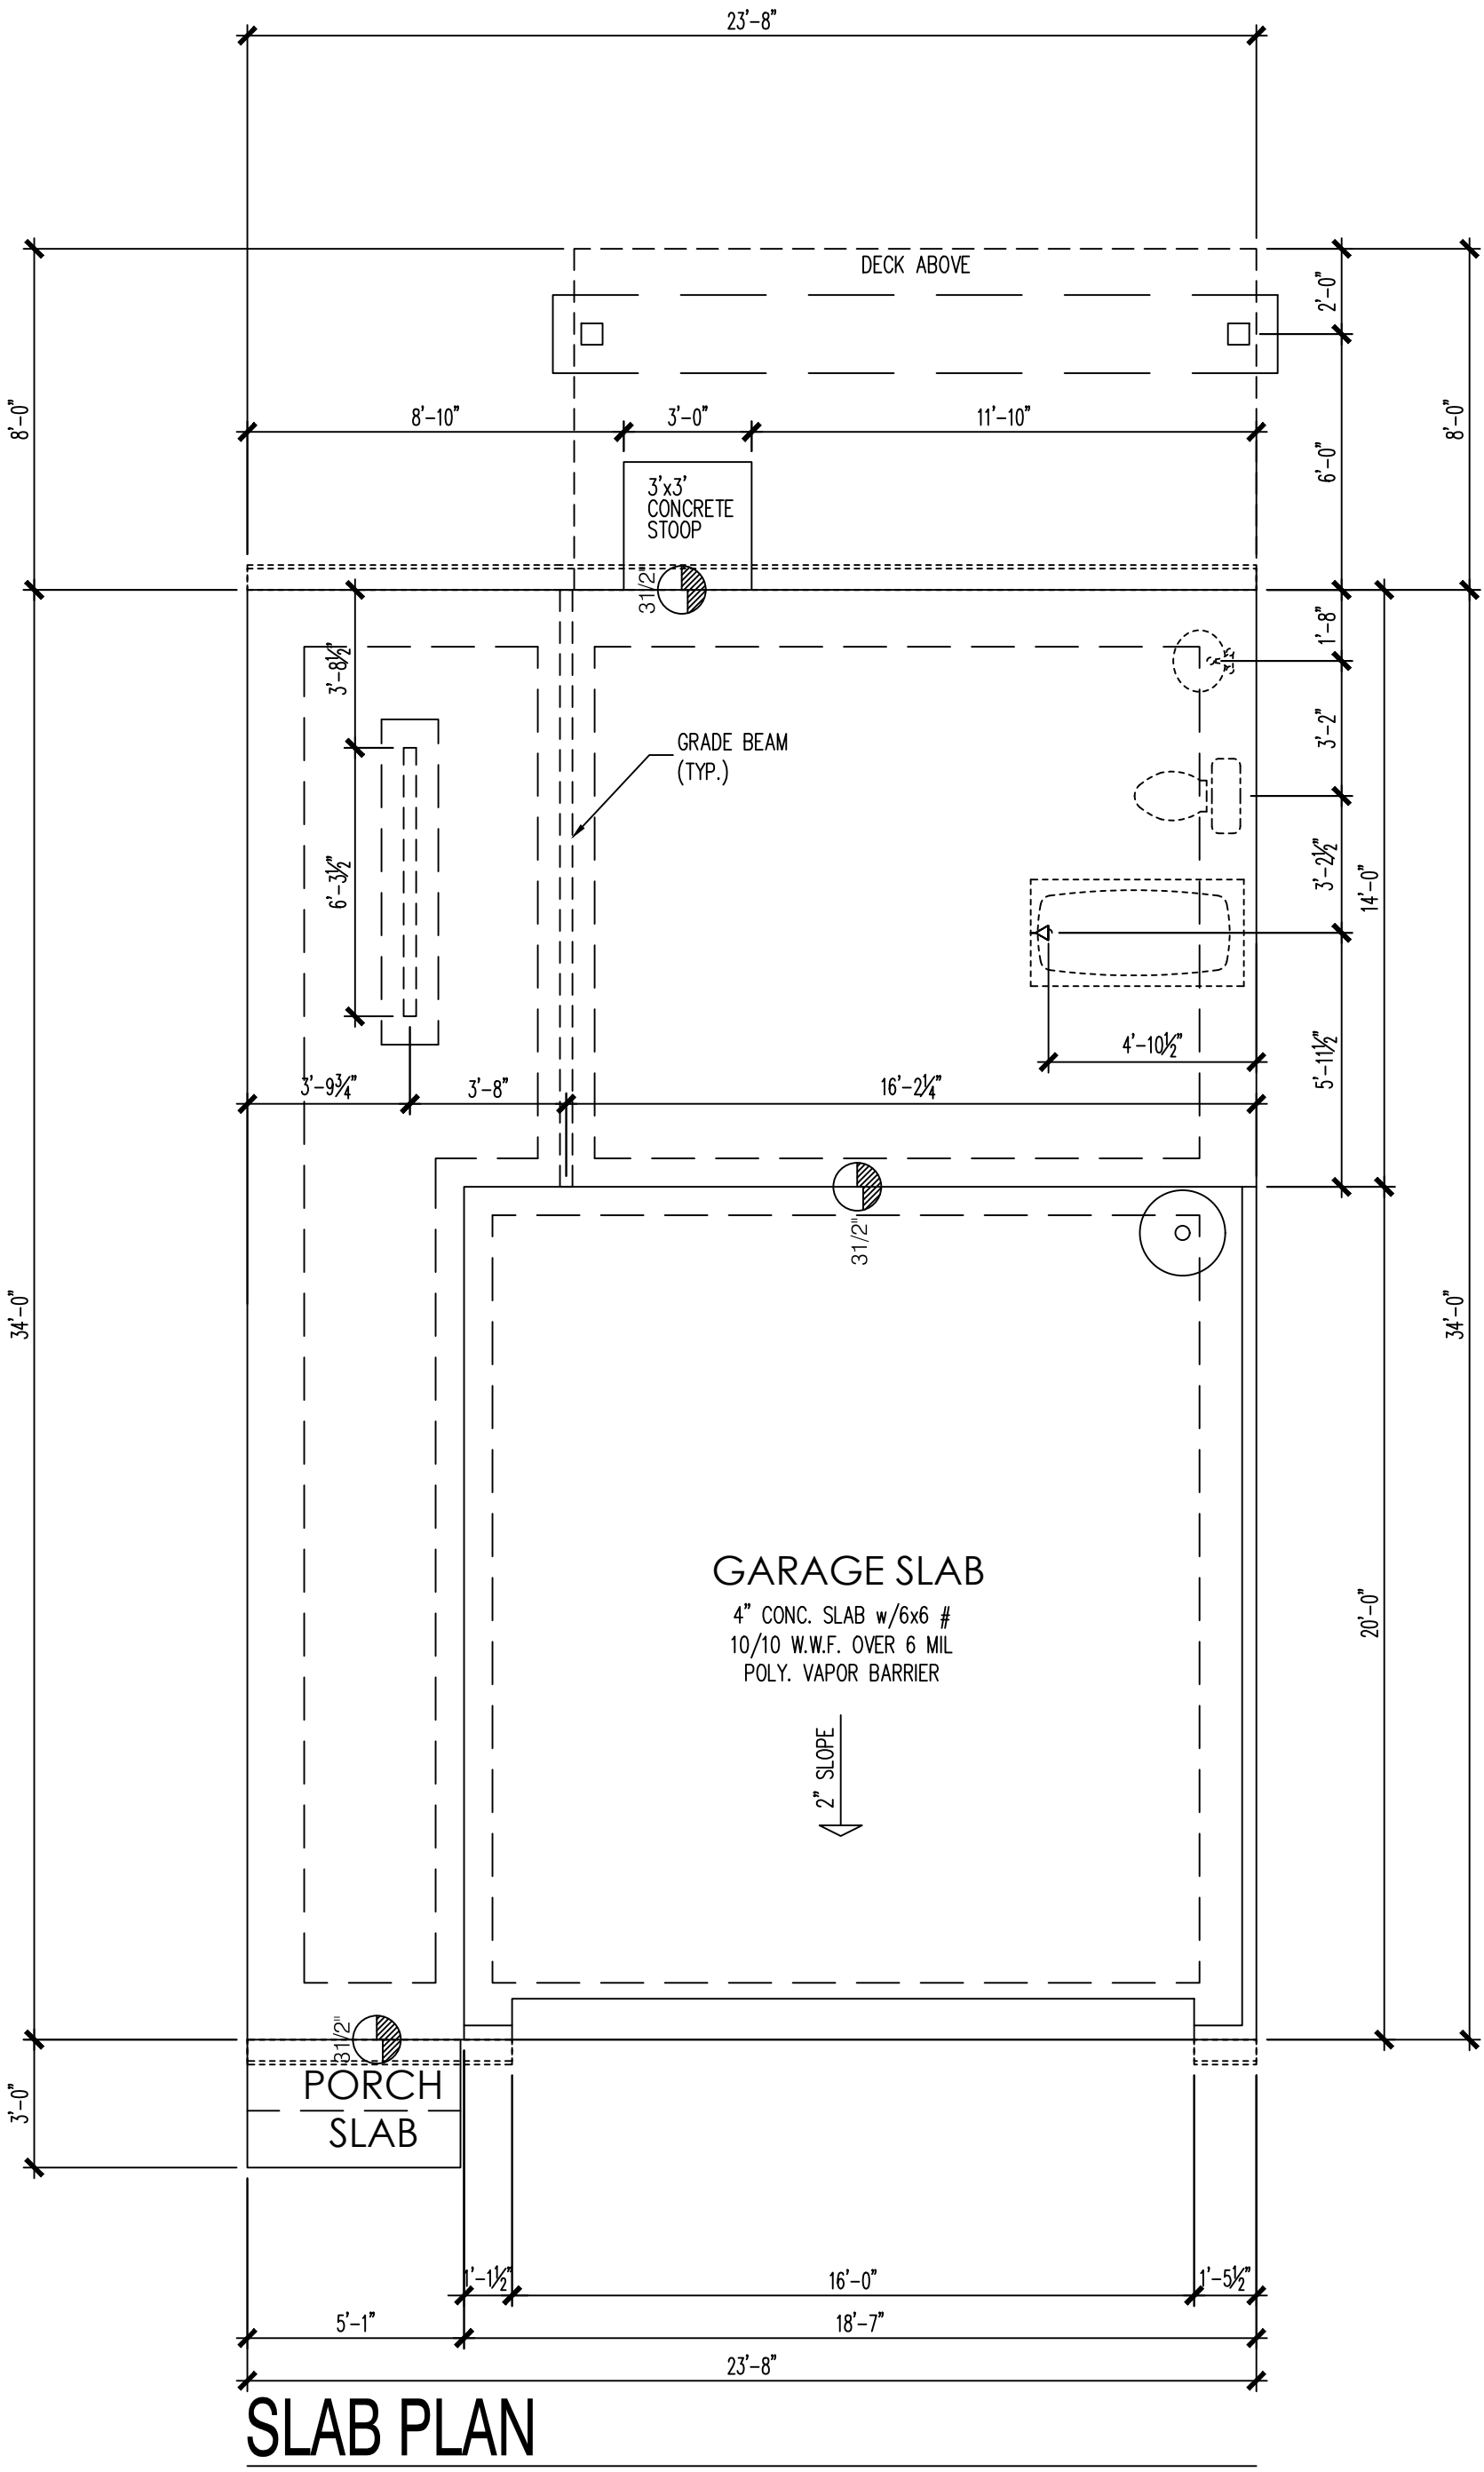

REVISIONS

No.	DESCRIPTION	No.	DESCRIPTION
1		6	
2		7	
3		8	
4		9	
5		10	


RELEASE FOR
CONSTRUCTION

PROJECT: SLAB & TERRACE FLR ASPEN

SHEET TITLE:

SLAB & GROUND

DESIGNED BY :	PLAN NAME:
DRAWN BY :	SCALE: 1/8"=1'-0"
CHECKED BY :	PRODUCT TYPE:
REVIEWED BY :	SHEET:
RELEASE DATE:	2.05

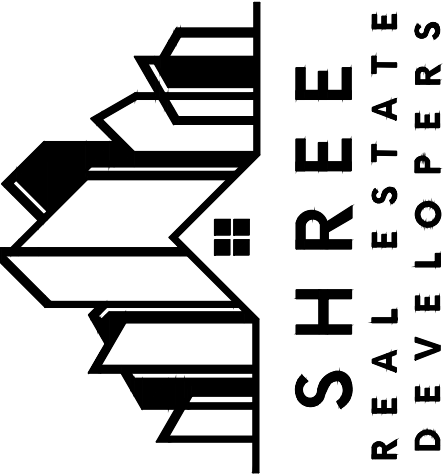

5400 LAUREL SPRINGS PKWY,
BLDG 700, STE 702
SUWANEE GA 30024
770-789-7044

CONSTRUCTION SHALL CONFORM WITH ALL APPLICABLE LOCAL CODES AND ORDINANCES

ALL WALLS ARE FRAMED W/ 2X4 STUDS U.N.O. W/ EXTERIOR & LOAD BEARING WALLS @ 16" O.C. INTERIOR NON-LOAD BEARING WALLS @ 24" O.C.

LOAD BEARING WALLS SYMBOL

=====

BALLOON FRAME ALL TWO STORY WALLS. PROVIDE WOOD BLOCKING BEHIND CEILING FANS

PROVIDE ADEQUATE BLOCKING FOR ALL WALL CABINETS.

CLOSETS TO HAVE 1 ROD AND 1 SHELF WHERE SHOWN UNLESS NOTED OTHERWISE

1R&1S - SHELF 69" A.F.F. 2R&1S-SHELF & 80" A.F.F. 2nd ROD 38" A.F.F.

LINEN CLOSETS AND PANTRIES TO HAVE (5) 16" DEEP SHELVES UNLESS NOTED OTHERWISE, FIRST SHELF TO BE @ 36" AFF W/ SHELF SPACING 12" O.C. ABV.

UTILITY ROOM TO HAVE (1) 16" SHELF AT 60" A.F.F. ABOVE WASHER & DRYER. CABINETS ARE PER COMMUNITY SPECS.

DOOR INTO THE HOUSE FROM THE GARAGE TO BE WEATHERSTRIPPED SOLID CORE

ALL MIRROR WIDTHS TO BE 3" LESS THAN OVERALL VANITY WIDTH. MIRROR HEIGHTS ARE PER COMMUNITY SPECS

CENTER OF TOILET TO BE A MIN. OF 15" FROM THE VERTICAL SURFACE OF SIDE WALLS, CABINETS OR OTHER OBSTRUCTION. PROVIDE A MIN OF 21" CLEAR FROM TOILET TO THE VERTICAL FACE OF A TUB OR OTHER OBSTRUCTION. EDGE OF TOILET TO BE A MIN. FO 4" FROM PEDESTAL OR WALL MOUNTED LAV.

FACE EDGE OF SHOWER UNITS TO HAVE A MIN. 24" CLEAR TO ANY VERTICAL SURFACE.

A/C PADS ARE TO BE 36"x36" OR 36"x72" FOR 2-UNIT A/C PAD

STUB GAS LINE 6" AFF AT CENTERLINE OF RANGE

FIRE CAULK ALL PLATE PENETRATIONS

FP ROUGH OPENING SCHEDULE		
FP BOX SIZE:	OPNG WIDTH:	OPNG HEIGHT:
36" BOX	42"	34 5/8"
42" BOX	48"	34 5/8"


HEADER SCHEDULE		
SPAN:	FRAMING:	LABEL:
UP TO 6'-6"	2-2x12	HDR-A
6'-7" TO 9'-0"	2-9 1/4" LVL	HDR-B
OVER 9'-0"	BY ENGINEER	ENG.

- | | |
|----|---|
| H1 | HEADER MATERIAL TO BE A MIN. # 2 S.Y.P. |
| H2 | PROVIDE 2-2x12 HEADERS AT ALL GARAGE DOOR OPENINGS AND WINDOWS 6'-0" OR GREATER. HEADERS, LONGER THAN 9'-0", IF NOT SPECIFIED ON PLANS, ARE TO BE DESIGNED BY A REGISTERED PROFESSIONAL ENGINEER. |
| H3 | LOCATE HEADER DIRECTLY ABOVE OPENING. PROVIDE CRIPPLE FRAMING FROM TOP PLATES TO HEADER AS REQUIRED. |
| H4 | TABLE APPLIES TO ALL EXTERIOR WALLS AND LOAD BEARING INTERIOR WALLS. FOR NON-LOAD BEARING INTERIOR WALLS, USE 2-2x4'S CUT FROM STUDS. |
| H5 | DO NOT USE TABLE IF HEADERS SUPPORT CONCENTRATED LOADS. |

D1	PROVIDE SITE DRAINAGE AS REQUIRE BY SITE TOPOGRAPHY
D2	FINISH FLOOR SHALL BE A MIN. OF 8" ABOVE ADJ. FINISH GRADE FINISH GRADE SHALL SLOPE 5% FOR A MIN. DISTANCE OF 10'-0" FROM HOUSE TO AN APPROVED DRAINAGE SYS.

CPT * WRF = FLOORING CHANGE LINE
WRF = WATER RESISTANT FLOORING
CPT = CARPET

PLUMBING FIXTURES WILL NOT PENETRATE
FIREWALLS UNDER ANY CIRCUMSTANCE

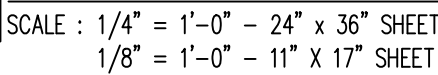

SCALE : $1/4" = 1'-0"$ - 24" x 36" SHEET
 $1/8" = 1'-0"$ - 11" x 17" SHEET

No.	DESCRIPTION	No.	DESCRIPTION
1		6	
2		7	
3		8	
4		9	
5		10	

RELEASE FOR
CONSTRUCTION

FLOOR PLANS

ASPEN

MAIN FLOOR

DESIGNED BY :	PLAN NAME:
DRAWN BY:	SCALE: 1/8" = 1'-0"
CHECKED BY:	PRODUCT TYPE:
REVIEWED BY:	SHEET: 21
RELEASE DATE:	



SCALE : $1/4" = 1'-0"$ - 24" x 36" SHEET
 $1/8" = 1'-0"$ - 11" x 17" SHEET

OPTIONAL FIREPLACE

SCALE : $1/4" = 1'-0"$ - 24" x 36" SHEET
 $1/8" = 1'-0"$ - 11" x 17" SHEET



SCALE : $1/4" = 1'-0"$ - 24" x 36" SHEET
 $1/8" = 1'-0"$ - 11" x 17" SHEET



SCALE : $1/4" = 1'-0"$ - 24" x 36" SHEET
 $1/8" = 1'-0"$ - 11" x 17" SHEET



SCALE : $1/4" = 1'-0"$ - 24" x 36" SHEET
 $1/8" = 1'-0"$ - 11" X 17" SHEET



REVISIONS

No.	DESCRIPTION	No.	DESCRIPTION
1		6	
2		7	
3		8	
4		9	
5		10	


RELEASE FOR
CONSTRUCTION

PROJECT: **FLOOR PLAN OPTIONS**

SHEET TITLE:

MAIN FLOOR

DESIGNED BY :	PLAN NAME:
DRAWN BY:	SCALE:
CHECKED BY:	1/8" = 1'-0"
REVIEWED BY:	PRODUCT TYPE:
RELEASE DATE:	SHEET:
	2.1.1

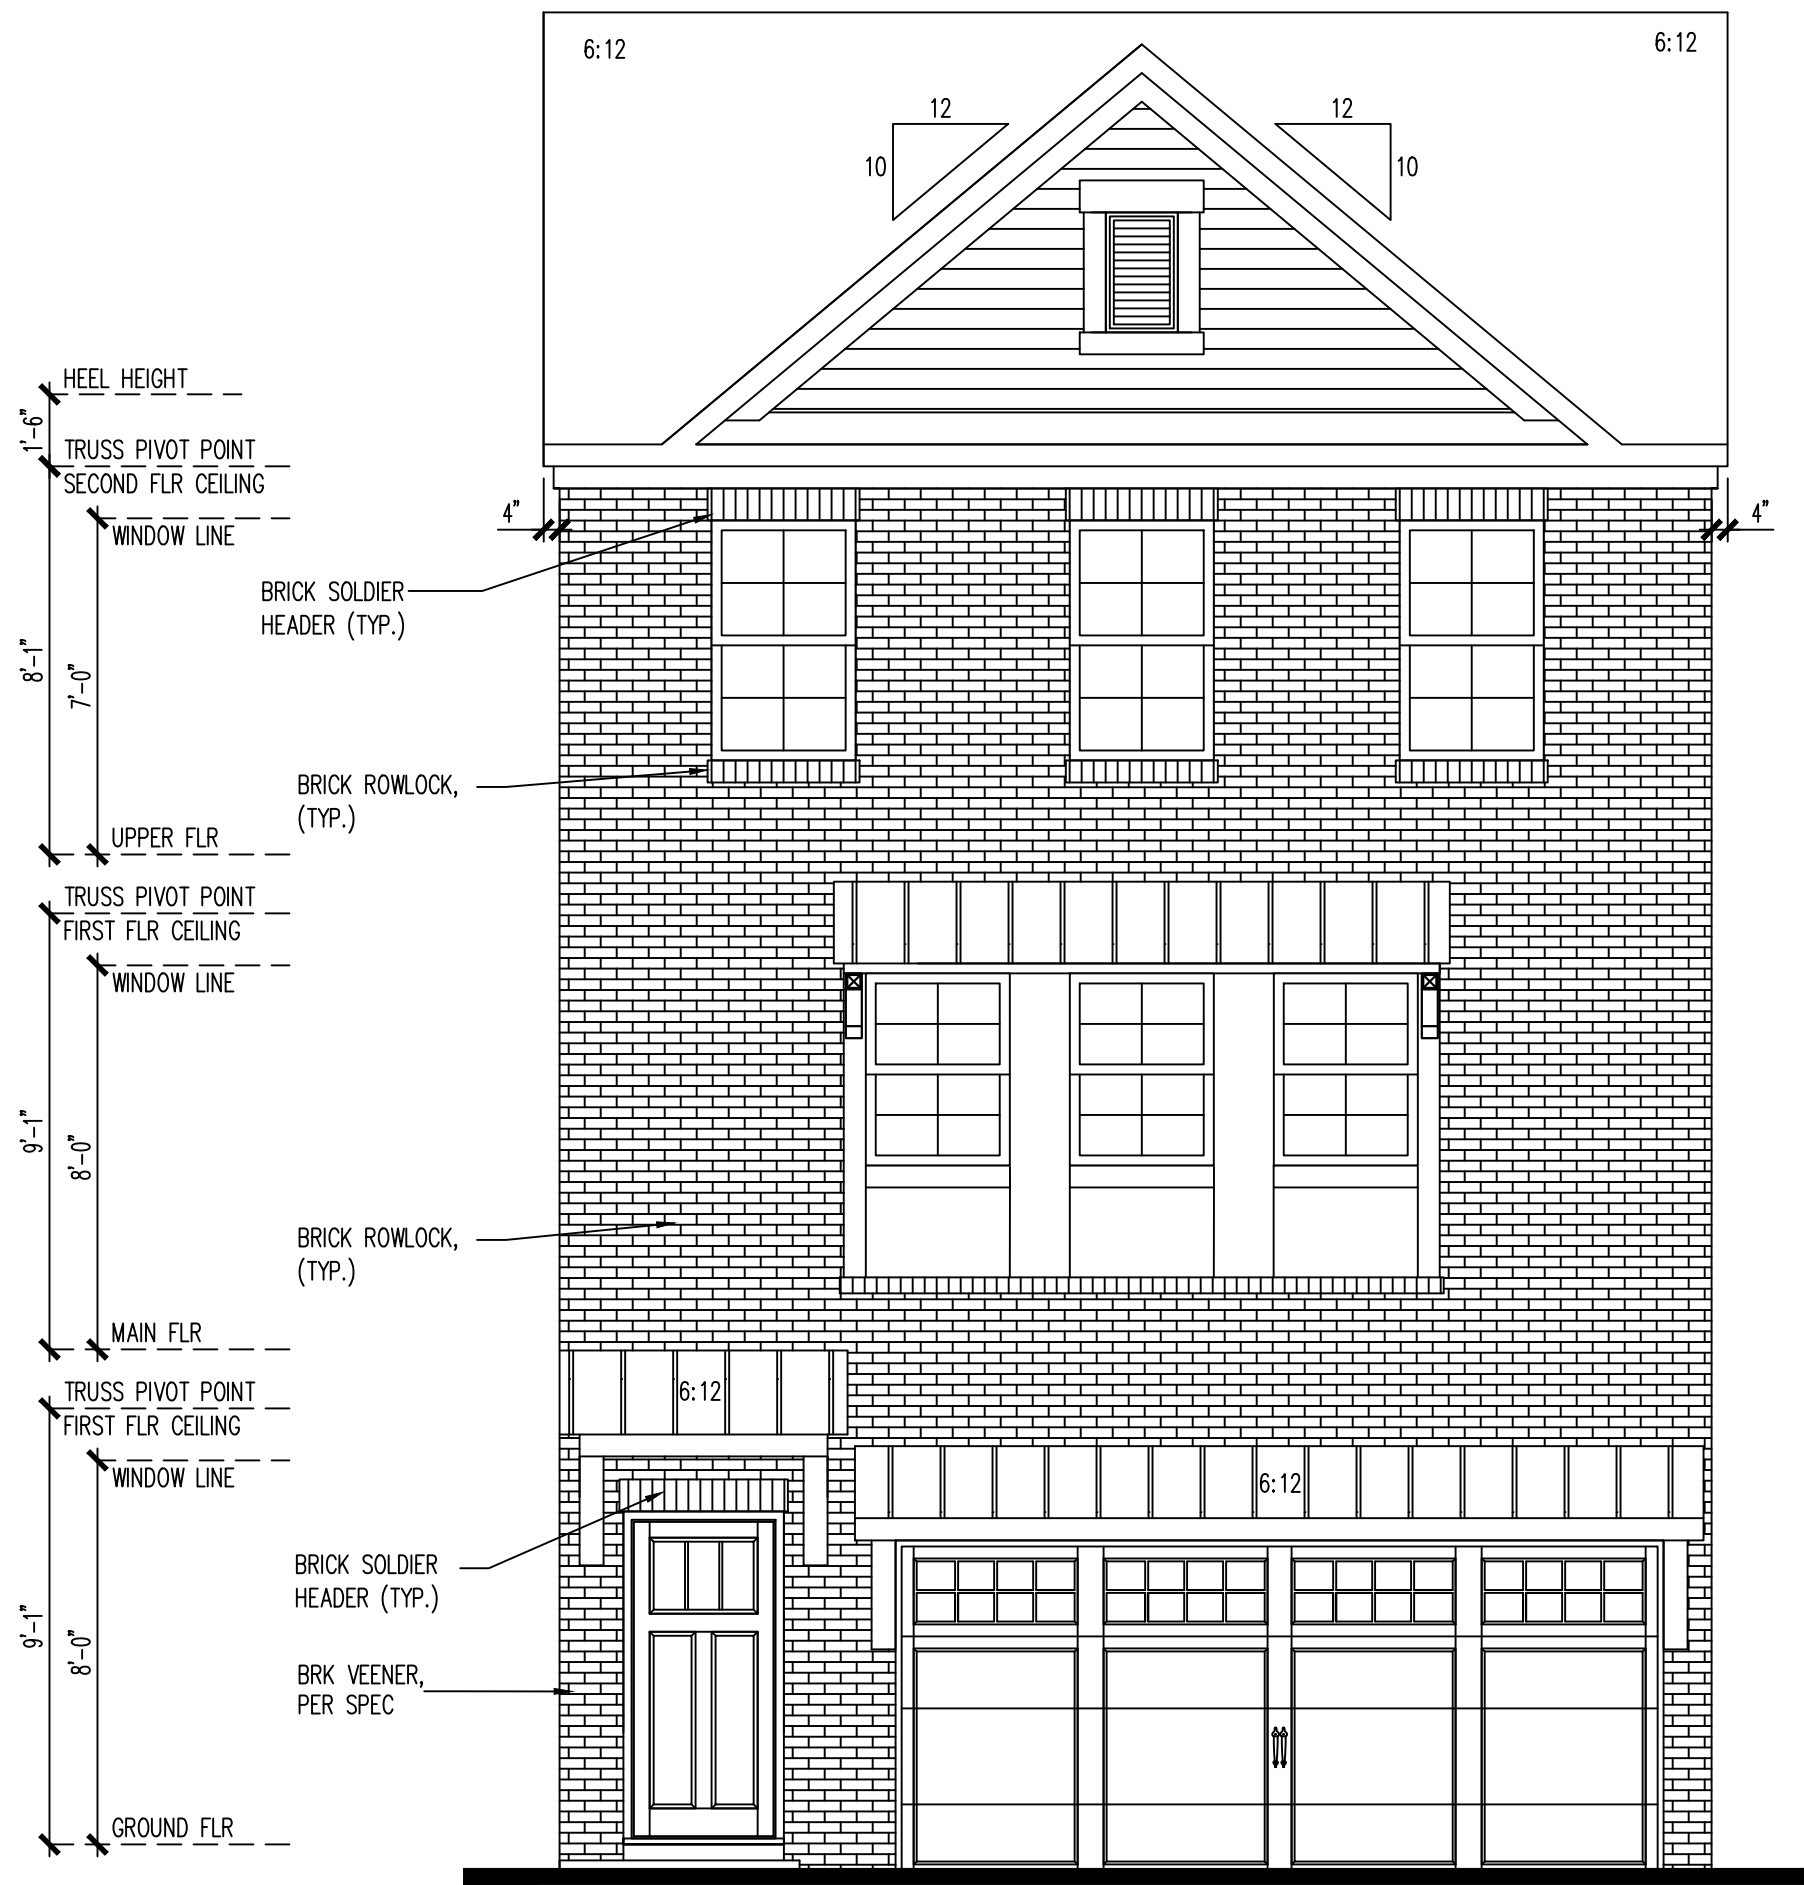


FRONT ELEVATION "11"

SCALE : 1/4" = 1'-0"



REAR ELEVATION "11"

SCALE : 1/4" = 1'-0"

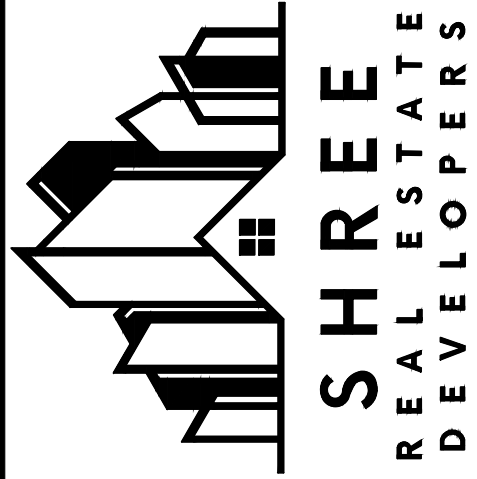

5400 LAUREL SPRINGS PKWY,
BLDG 700, STE 702
SUWANEE GA 30024
770-789-7044

REVISIONS			
No	DESCRIPTION	No	DESCRIPTION
1		6	
2		7	
3		8	
4		9	
5		10	

RELEASE FOR
CONSTRUCTION

PROJECT:
FRONT & REAR ELEVS
ASPEN

SHEET TITLE:
ELEV. "11"

DESIGNED BY :	PLAN NAME:
DRAWN BY :	SCALE: 1/8"=1'-0"
CHECKED BY :	PRODUCT TYPE:
REVIEWED BY :	SHEET:
RELEASE DATE:	3.11



HEEL HEIGHT
1'-6"

TRUSS PIVOT POINT
SECOND FLR CEILING
8'-1"

WINDOW LINE
7'-0"

UPPER FLR
9'-1"

TRUSS PIVOT POINT
FIRST FLR CEILING
8'-0"


WINDOW LINE
8'-0"

MAIN FLR
9'-1"

TRUSS PIVOT POINT
FIRST FLR CEILING
8'-0"

WINDOW LINE
8'-0"

GROUND FLR

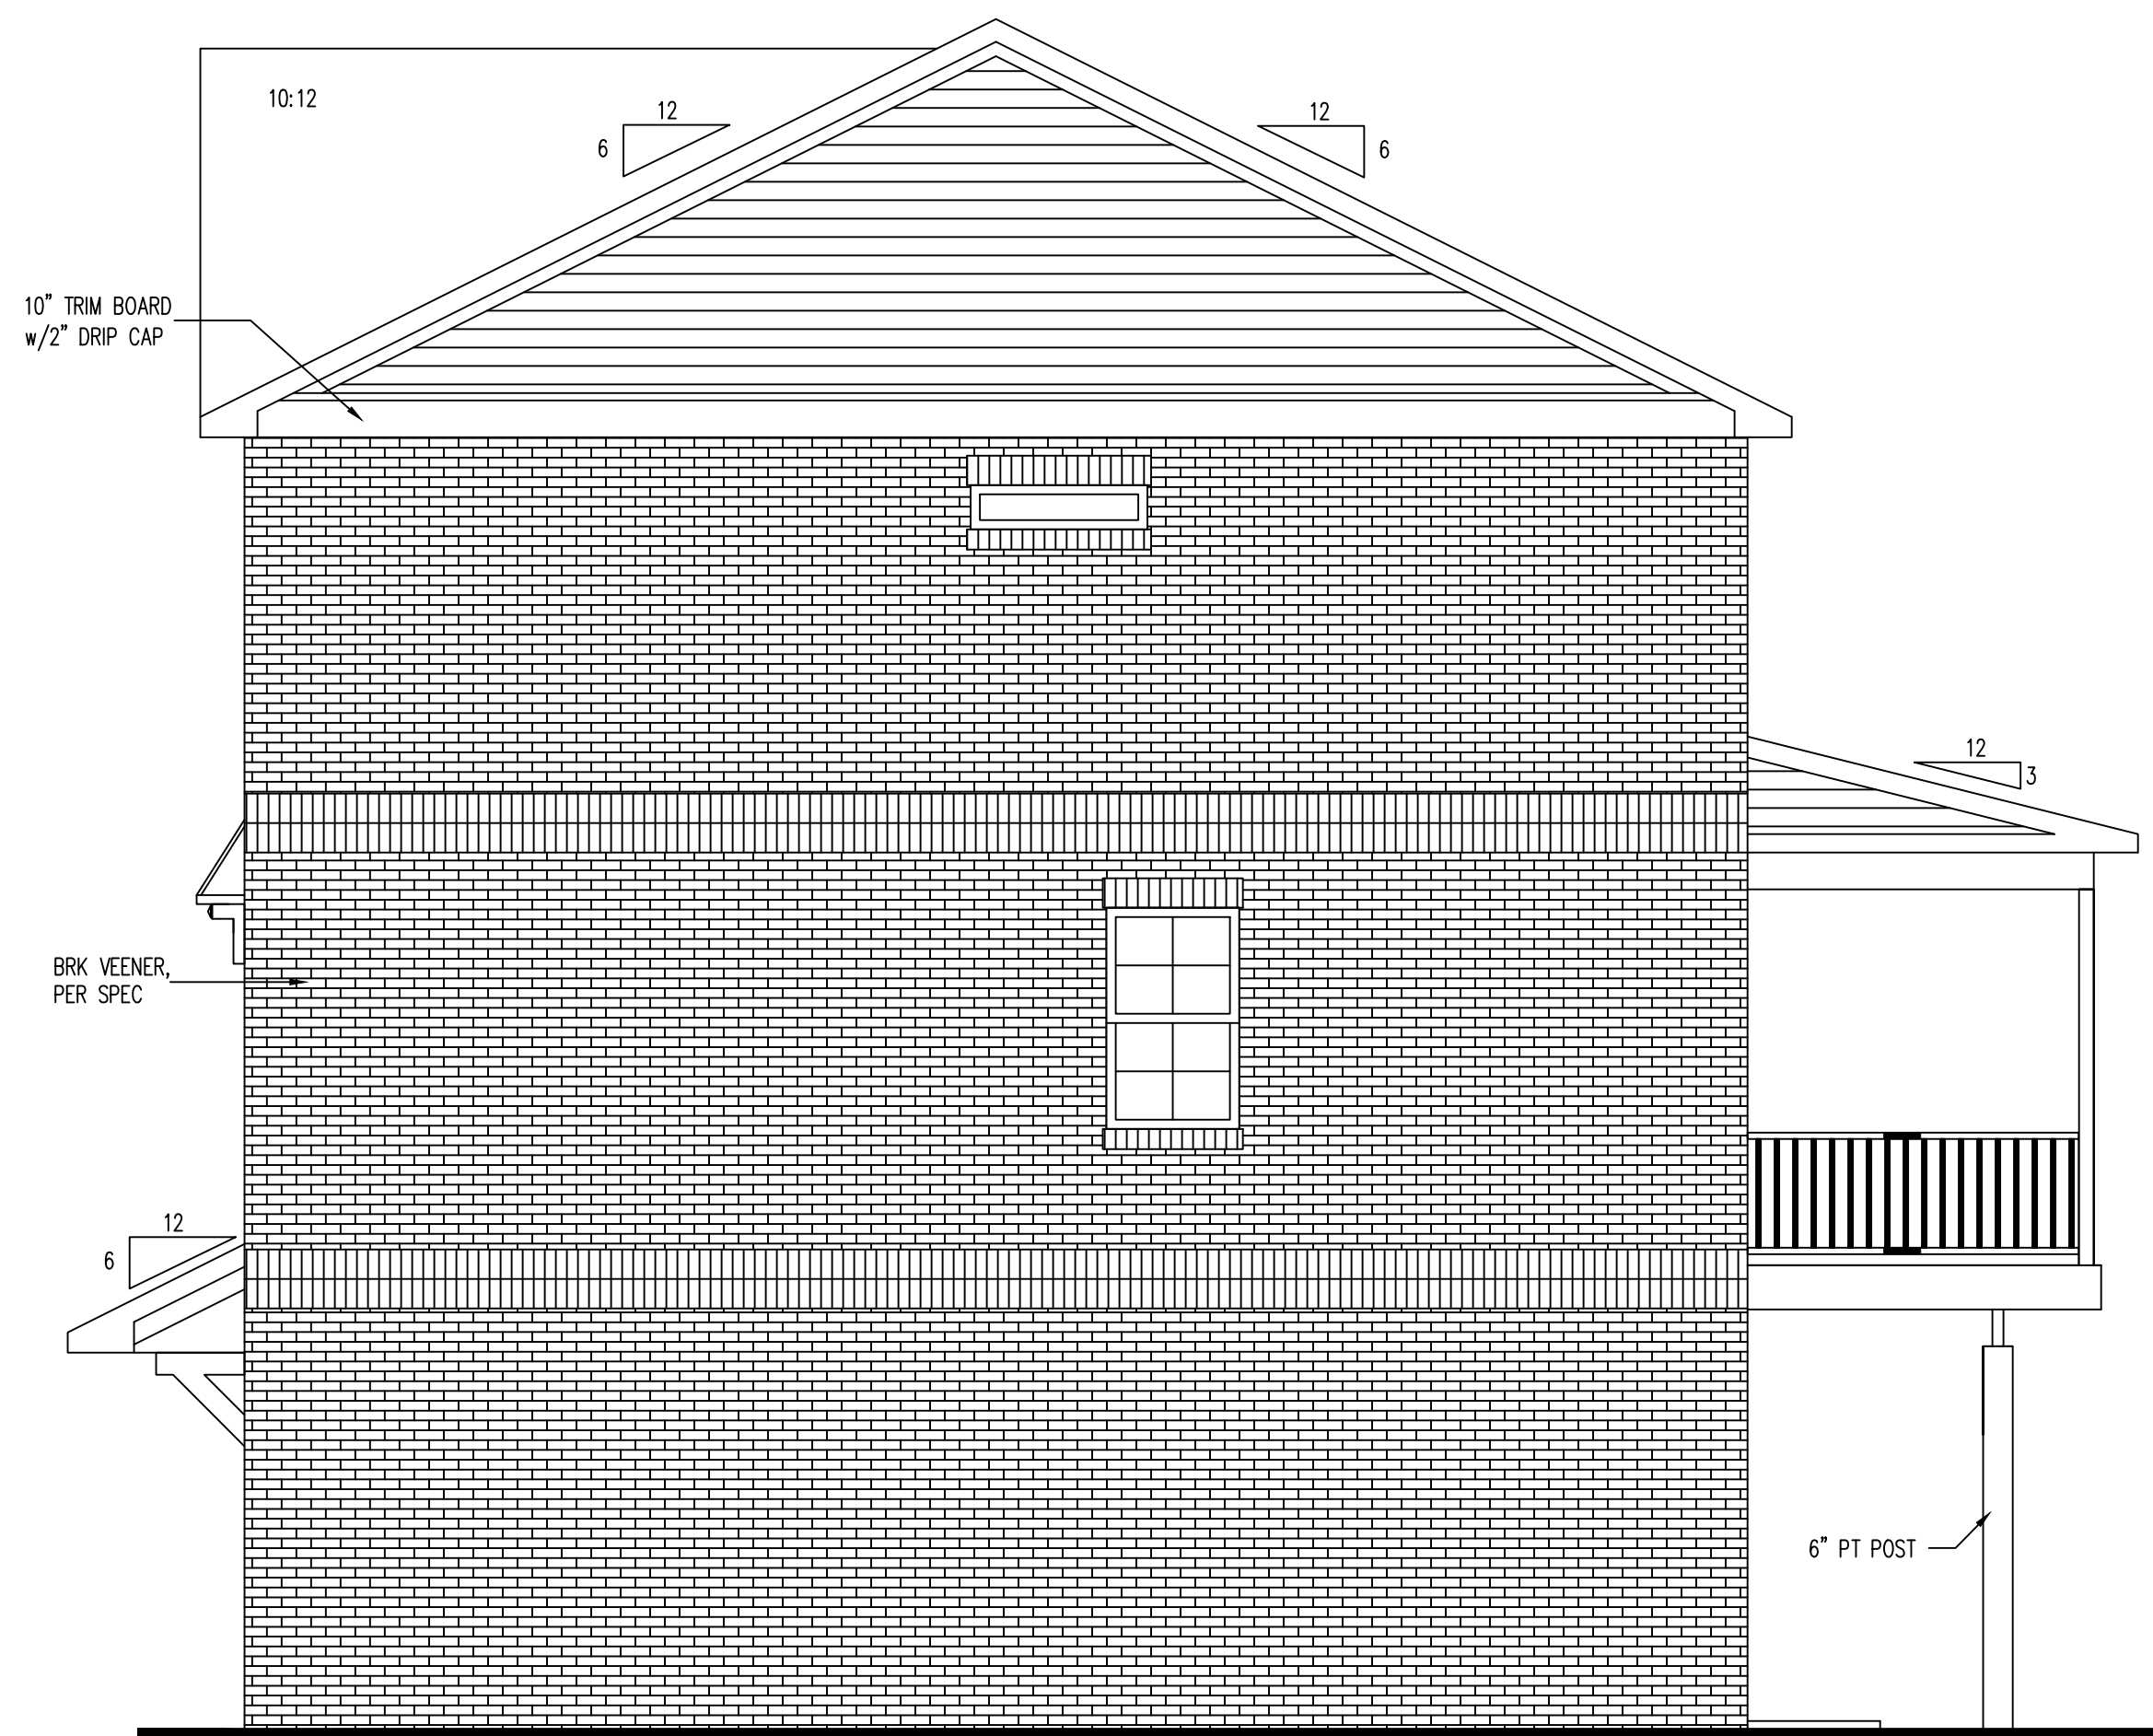

RIGHT ELEVATION "11"

ROOF PLAN



SHREE
REAL ESTATE
DEVELOPERS

REVISIONS

No.	DESCRIPTION	No.	DESCRIPTION
1		6	
2		7	
3		8	
4		9	
5		10	

RELEASE FOR
CONSTRUCTION

PROJECT:

SIDE ELEVATIONS

ASPEN


SHEET TITLE:


ELEV. "22"

DESIGNED BY:	PLAN NAME:
DRAWN BY:	SCALE: 1/8" = 1'-0"
CHECKED BY:	PRODUCT TYPE:
REVIEWED BY:	SHEET: 3.12
RELEASE DATE:	

ELECTRICAL NOTES:


- E1ELECTRICAL INSTALLATION TO BE IN ACCORDANCE WITH THE NATIONAL ELECTRICAL CODE, NFPA-70.
- E2THE ELECTRICAL CONTRACTOR IS RESPONSIBLE FOR OBTAINING ELECTRICAL PERMITS AND INSPECTIONS
- E3CONVENIENCE RECEPTACLE - MOUNT AT 12" A.F.F. UNLESS NOTED OTHERWISE
- E4SWITCHES - MOUNT AT 48" A.F.F. AND LOCATED WITHIN 6" OF DOOR OR OPENING
- E5MICROWAVE OVEN - SEPARATE 20 AMP SINGLE RECEPTACLE AT 78" A.F.F..
- E6BATHROOM RECEPTACLES - GFI MOUNT 42" A.F.F.
- E7RECEPTACLES IN THE GARAGE TO BE GFI UNLESS NOTED FOR APPLIANCES
- E8EXTERIOR RECEPTACLES TO BE GFI AND WEATHER PROTECTED
- E9WASHER/DRYER - SEPARATE 20 AMP DUPLEX RECEPTACLE AT 44" A.F.F.
- E10TELEPHONE OUTLETS - PROVIDE BOX (MOUNT AT 12" A.F.F. UNLESS NOTED OTHERWISE), COVER PLATE, 4/C WIRE. TERMINATE NEAR PANEL
- E11KITCHEN COUNTER AND REFRIGERATOR RECEPTACLES AND APPLIANCE SWITCHES MOUNT AT 44" A.F.F.
- E12WALL LIGHT FIXWRFURE @ 7'-0" A.F.F. A.F.F. (STYLE PER SPEC. LEVEL.)
- E13SMOKE DETECTORS - INSTALL SMOKE DETECTORS IN ALL SLEEPING AREAS A MIN. OF 3'-0" FROM DUCT OPENINGS AND A MIN. OF 10'-0" FROM SLEPING ROOM DOORS. PROVIDE DETECTORS ON EACH STORY INCLUDING BASEMENTS. ALL SMOKE DETECTORS ARE TO BE INTERCONNECTED BY PERMANENTLY WIRING AND HAVE BATTERY BACK-UPS.

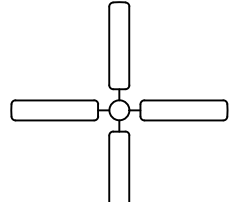ELECTRICAL LEGEND	
	DUPLEX OUTLET
	SWITCHED DUPLEX OUTLET
	GFI OUTLET
	WATER-PROOF GFI OUTLET
	CEILING MOUNTED OUTLET
	220V OULET
	VENT FAN
	SWITCH
	3-WAY SWITCH
	4-WAY SWITCH
	CEILING MOUNTED LIGHT
	RECESSED CEILING LIGHT
	WALL MOUNTED LIGHT
	CEILING FAN W/ LIGHT PER SPEC
	SMOKE DETECTOR
	TELEPHONE OUTLET
	CABLE TV OUTLET
	FLOOD LIGHT
	ELECTRICAL PANEL
	THERMOSTAT
	DOOR CHIMES

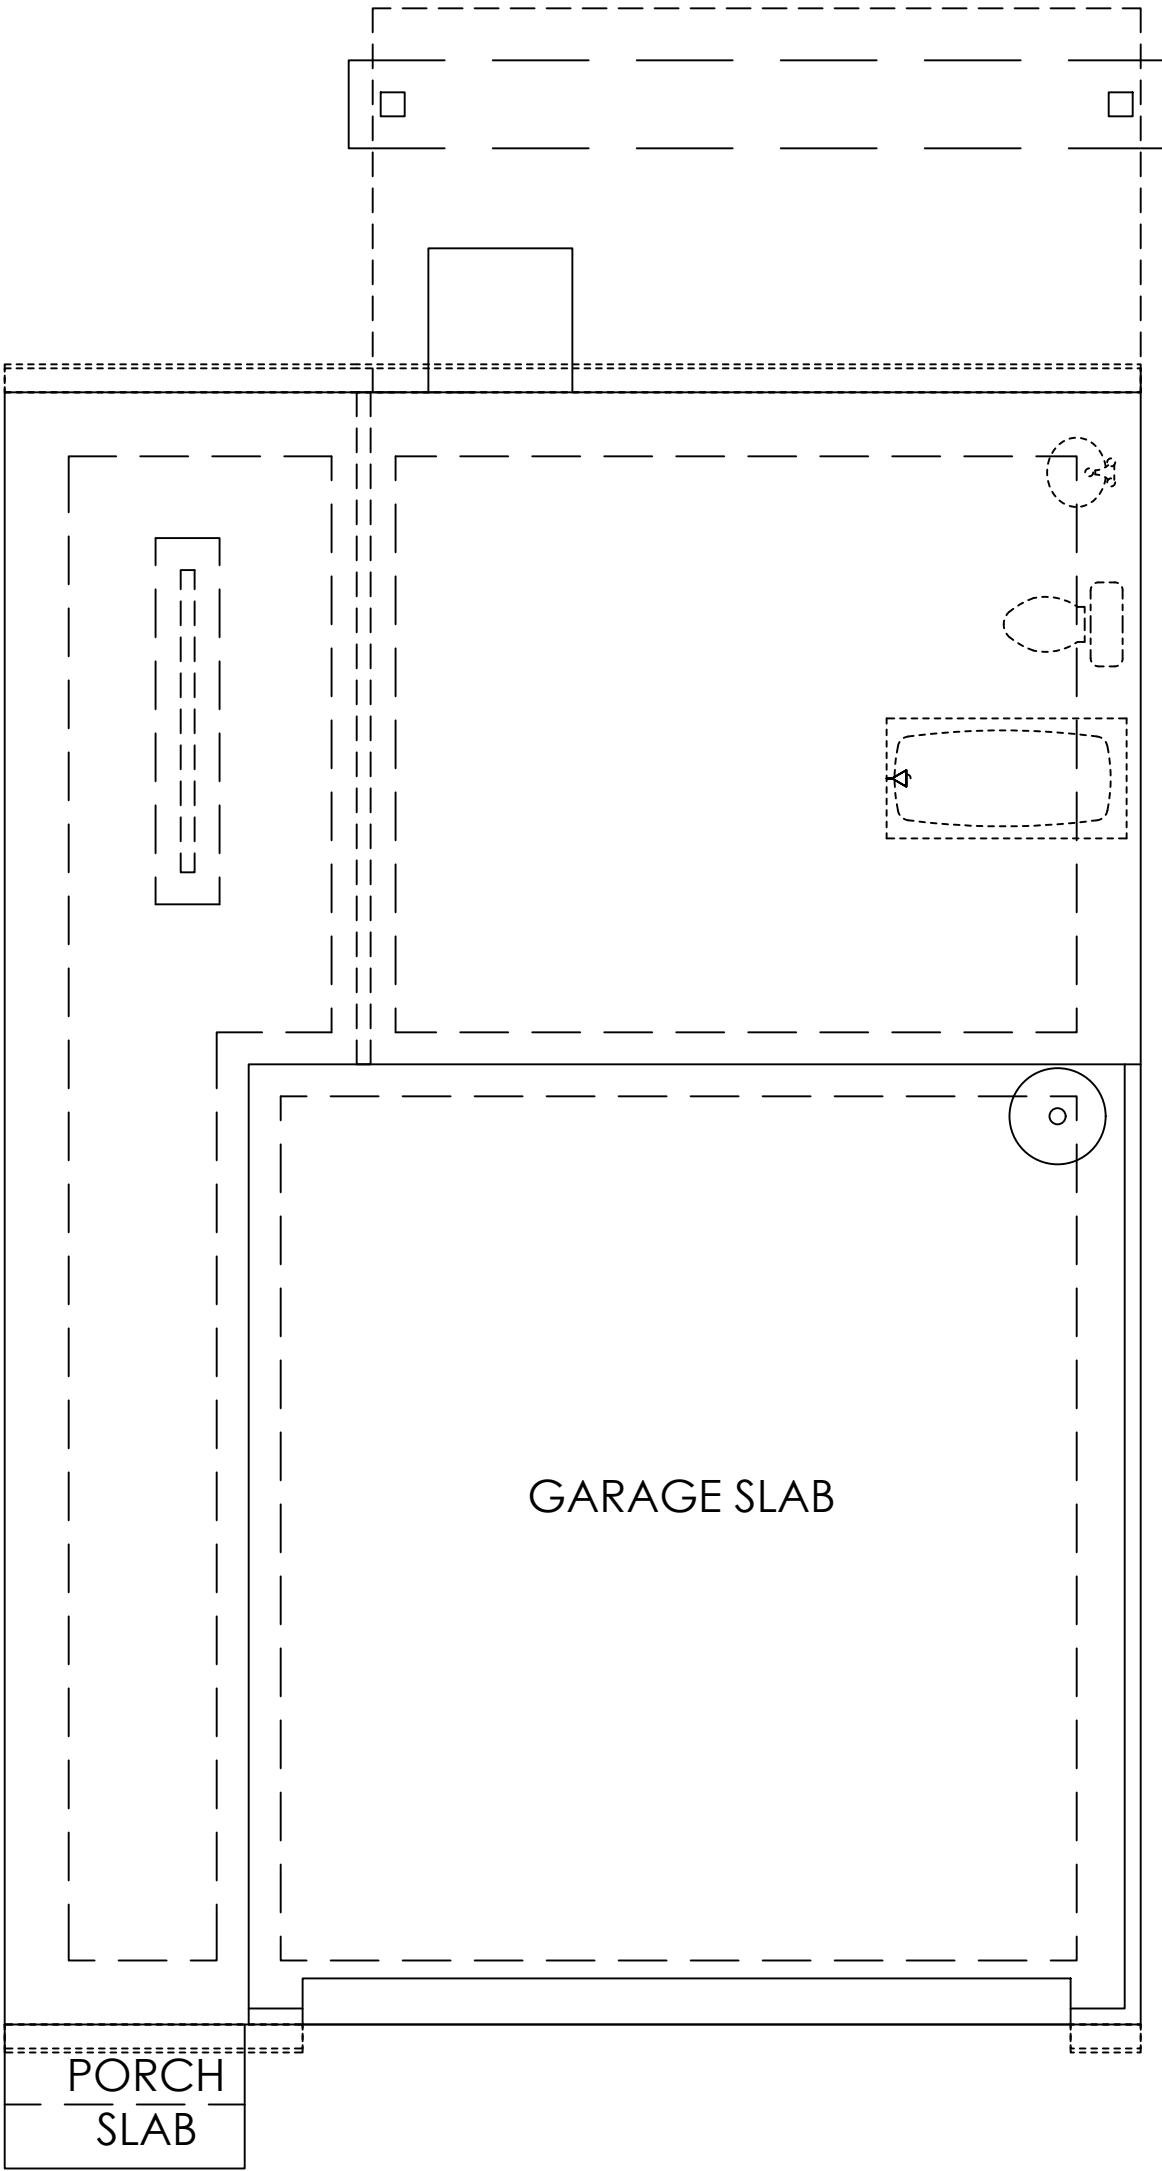

SLAB PLAN

SCALE : 1/4" = 1'-0" ~ 24" x 36" SHEET
1/8" = 1'-0" ~ 11" X 17" SHEET

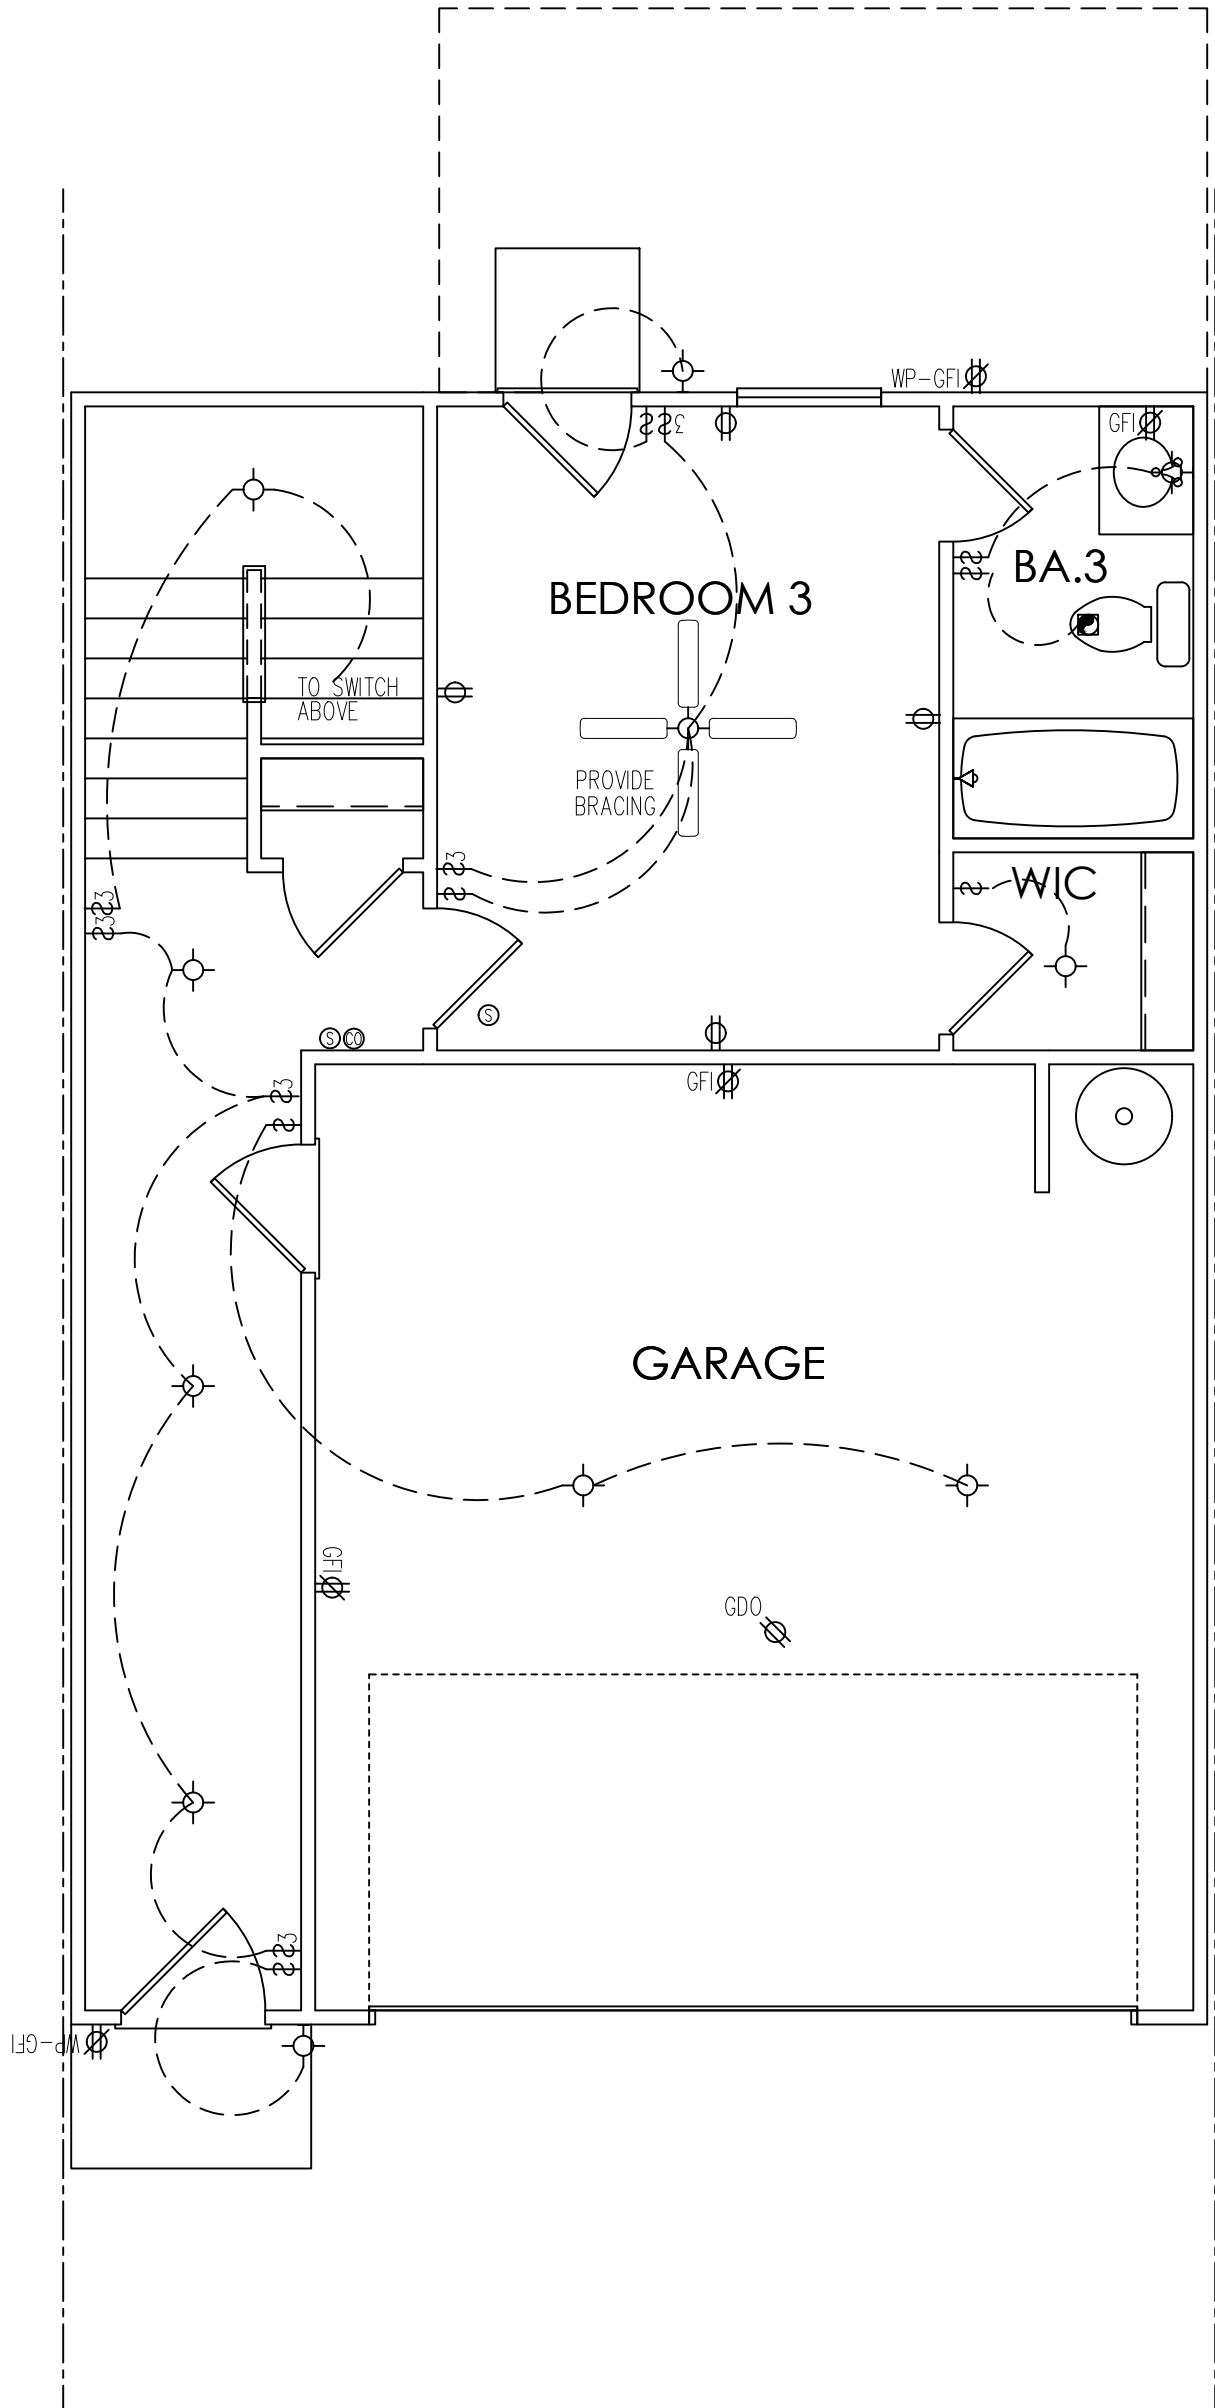

TERRACE PLAN

SCALE : 1/4" = 1'-0" ~ 24" x 36" SHEET
1/8" = 1'-0" ~ 11" X 17" SHEET

REVISIONS


No	DESCRIPTION	No	DESCRIPTION
1		6	
2		7	
3		8	
4		9	
5		10	

RELEASE FOR
CONSTRUCTION

PROJECT:
TERRACE FLR ELEC.
ASPEN

SHEET TITLE:
ELECTRICAL

DESIGNED BY :	PLAN NAME:
DRAWN BY :	SCALE: 1/8"=1'-0"
CHECKED BY :	PRODUCT TYPE:
REVIEWED BY :	SHEET: 5.0
RELEASE DATE:	

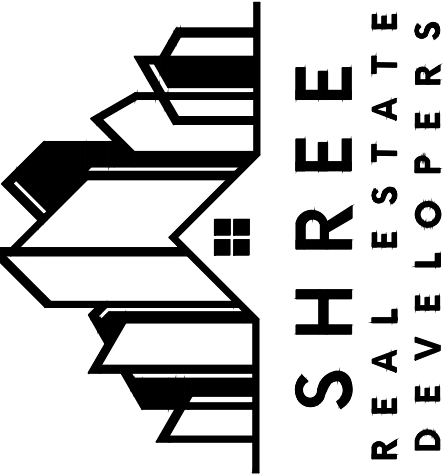

5400 LAUREL SPRINGS PKWY,
BLDG 700, STE 702
SUWANEE GA 30024
770-789-7044

ELECTRICAL NOTES:

- E1ELECTRICAL INSTALLATION TO BE IN ACCORDANCE WITH THE NATIONAL ELECTRICAL CODE, NFPA-70.
- E2THE ELECTRICAL CONTRACTOR IS RESPONSIBLE FOR OBTAINING ELECTRICAL PERMITS AND INSPECTIONS
- E3CONVENIENCE RECEPTACLE - MOUNT AT 12" A.F.F. UNLESS NOTED OTHERWISE
- E4SWITCHES - MOUNT AT 48" A.F.F. AND LOCATED WITHIN 6' OF DOOR OR OPENING
- E5MICROWAVE OVEN - SEPARATE 20 AMP SINGLE RECEPTACLE AT 78" A.F.F..
- E6BATHROOM RECEPTACLES - GFI MOUNT 42" A.F.F.
- E7RECEPTACLES IN THE GARAGE TO BE GFI UNLESS NOTED FOR APPLIANCES
- E8EXTERERIOR RECEPTACLES TO BE GFI AND WEATHER PROTECTED
- E9WASHER/DRYER - SEPARATE 20 AMP DUPLEX RECEPTACLE AT 44" A.F.F.
- E10TELEPHONE OUTLETS - PROVIDE BOX (MOUNT AT 12" A.F.F. UNLESS NOTED OTHERWISE), COVER PLATE, 4/C WIRE. TERMINATE NEAR PANEL
- E11KITCHEN COUNTER AND REFRIGERATOR RECEPTACLES AND APPLIANCE SWITCHES MOUNT AT 44" A.F.F.
- E12WALL LIGHT FIXWRFFURE @ 7'-0" A.F.F. A.F.F. (STYLE PER SPEC. LEVEL.)
- E13SMOKE DETECTORS - INSTALL SMOKE DETECTORS IN ALL SLEEPING AREAS A MIN. OF 3'-0" FROM DUCT OPENINGS AND A MIN. OF 10'-0" FROM SLEEPING ROOM DOORS. PROVIDE DETECTORS ON EACH STORY INCLUDING BASEMENTS. ALL SMOKE DETECTORS ARE TO BE INTERCONNECTED BY PERMANENTLY WIRING AND HAVE BATTERY BACK-UPS.

ELECTRICAL
LEGEND

DUPLEX OUTLET

SWITCHED DUPLEX OUTLET

GFI OUTLET

WATER-PROOF GFI OUTLET

CEILING MOUNTED OUTLET

220V OULET

VENT FAN

SWITCH


3-WAY SWITCH

4-WAY SWITCH

CEILING MOUNTED LIGHT

RECESSED CEILING LIGHT

WALL MOUNTED LIGHT

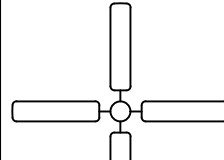CEILING FAN W/ LIGHT PER SPEC

SMOKE DETECTOR

TELEPHONE OUTLET



CABLE TV OUTLET

FLOOD LIGHT


ELECTRICAL PANEL

THERMOSTAT

DOOR CHIMES

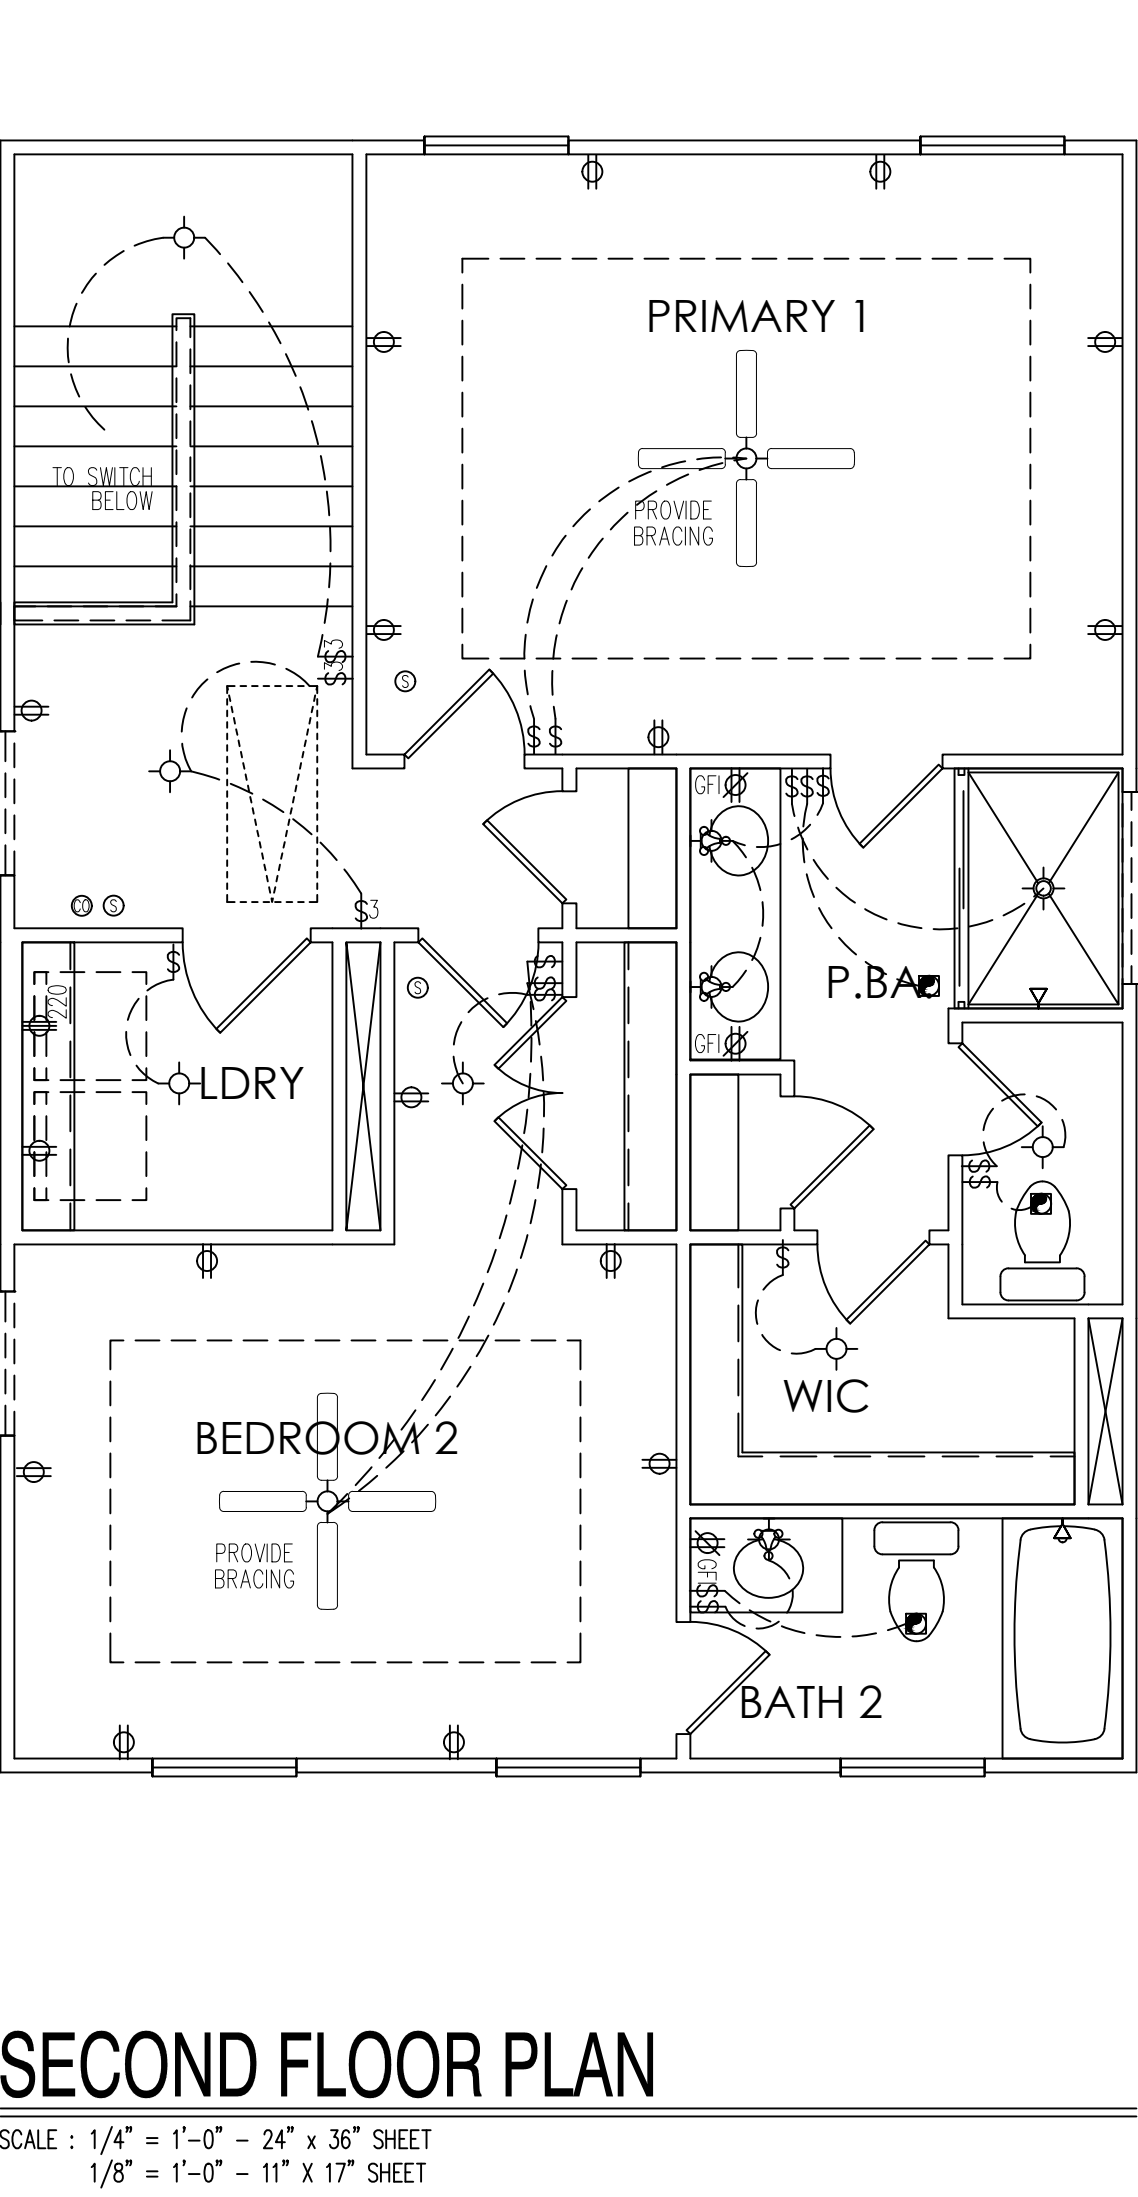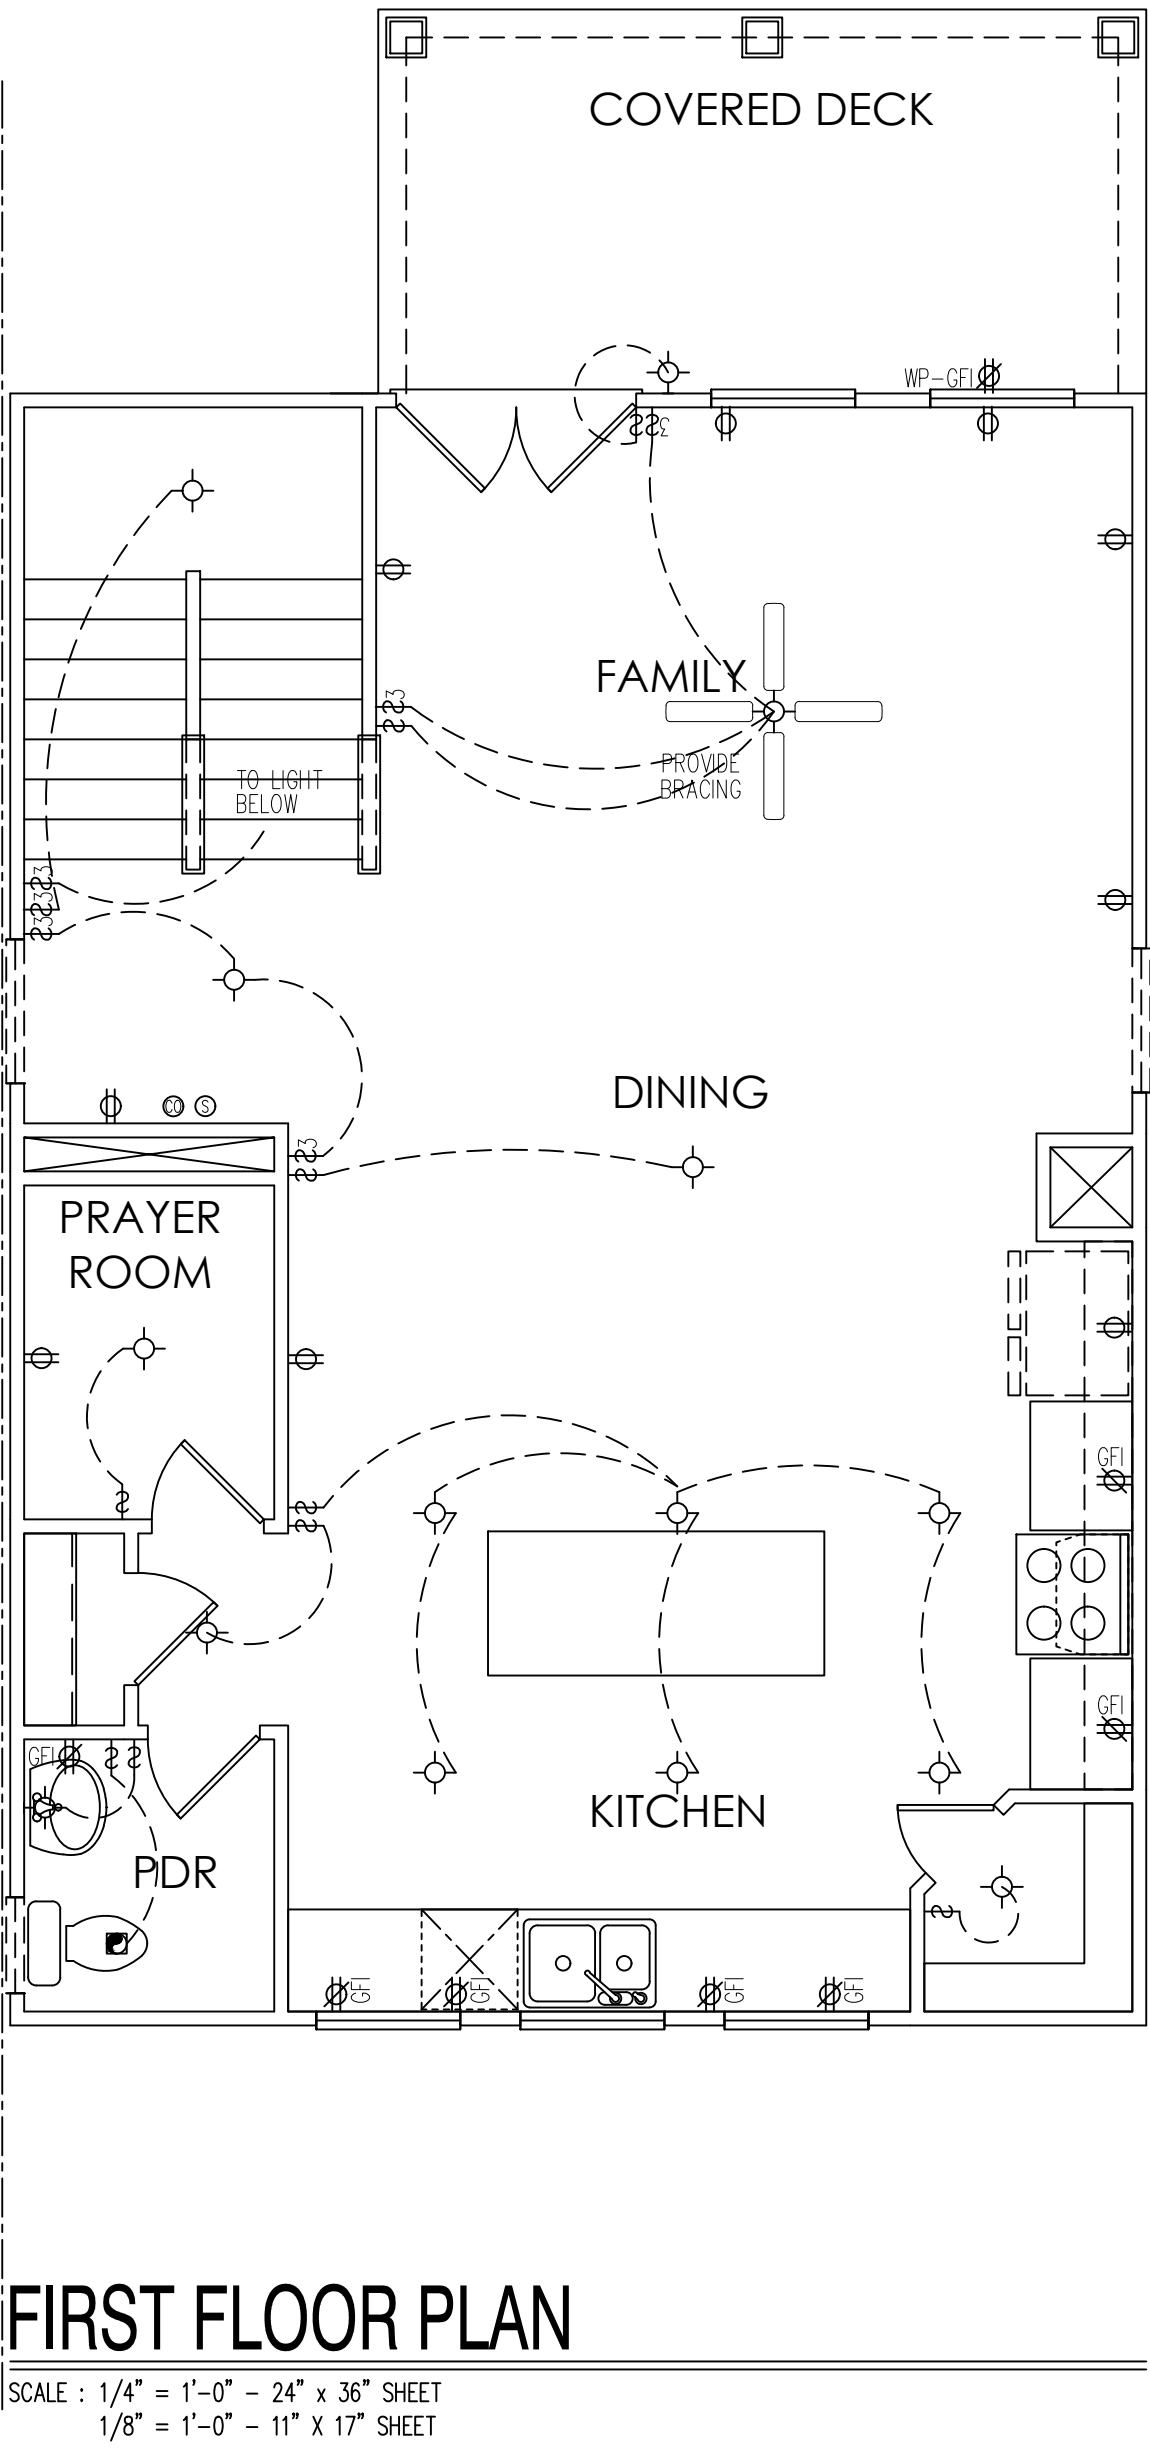

5400 LAUREL SPRINGS PKWY,
BLDG 700, STE 702
SUWANEE GA 30024
770-789-7044

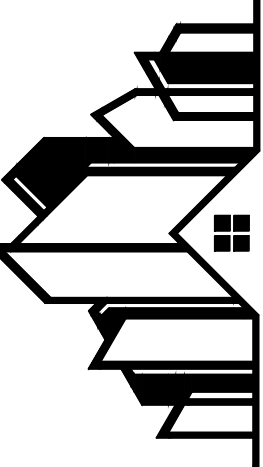SHREE
REAL ESTATE
DEVELOPERS

REVISIONS


No	DESCRIPTION	No	DESCRIPTION
1		6	
2		7	
3		8	
4		9	
5		10	

RELEASE FOR
CONSTRUCTION

PROJECT:
FLOOR PLANS ELEC.
ASPEN

SHEET TITLE:
ELECTRICAL

DESIGNED BY :	PLAN NAME:
DRAWN BY :	SCALE: 1/8"=1'-0"
CHECKED BY :	PRODUCT TYPE:
REVIEWED BY :	SHEET: 5.1
RELEASE DATE:	

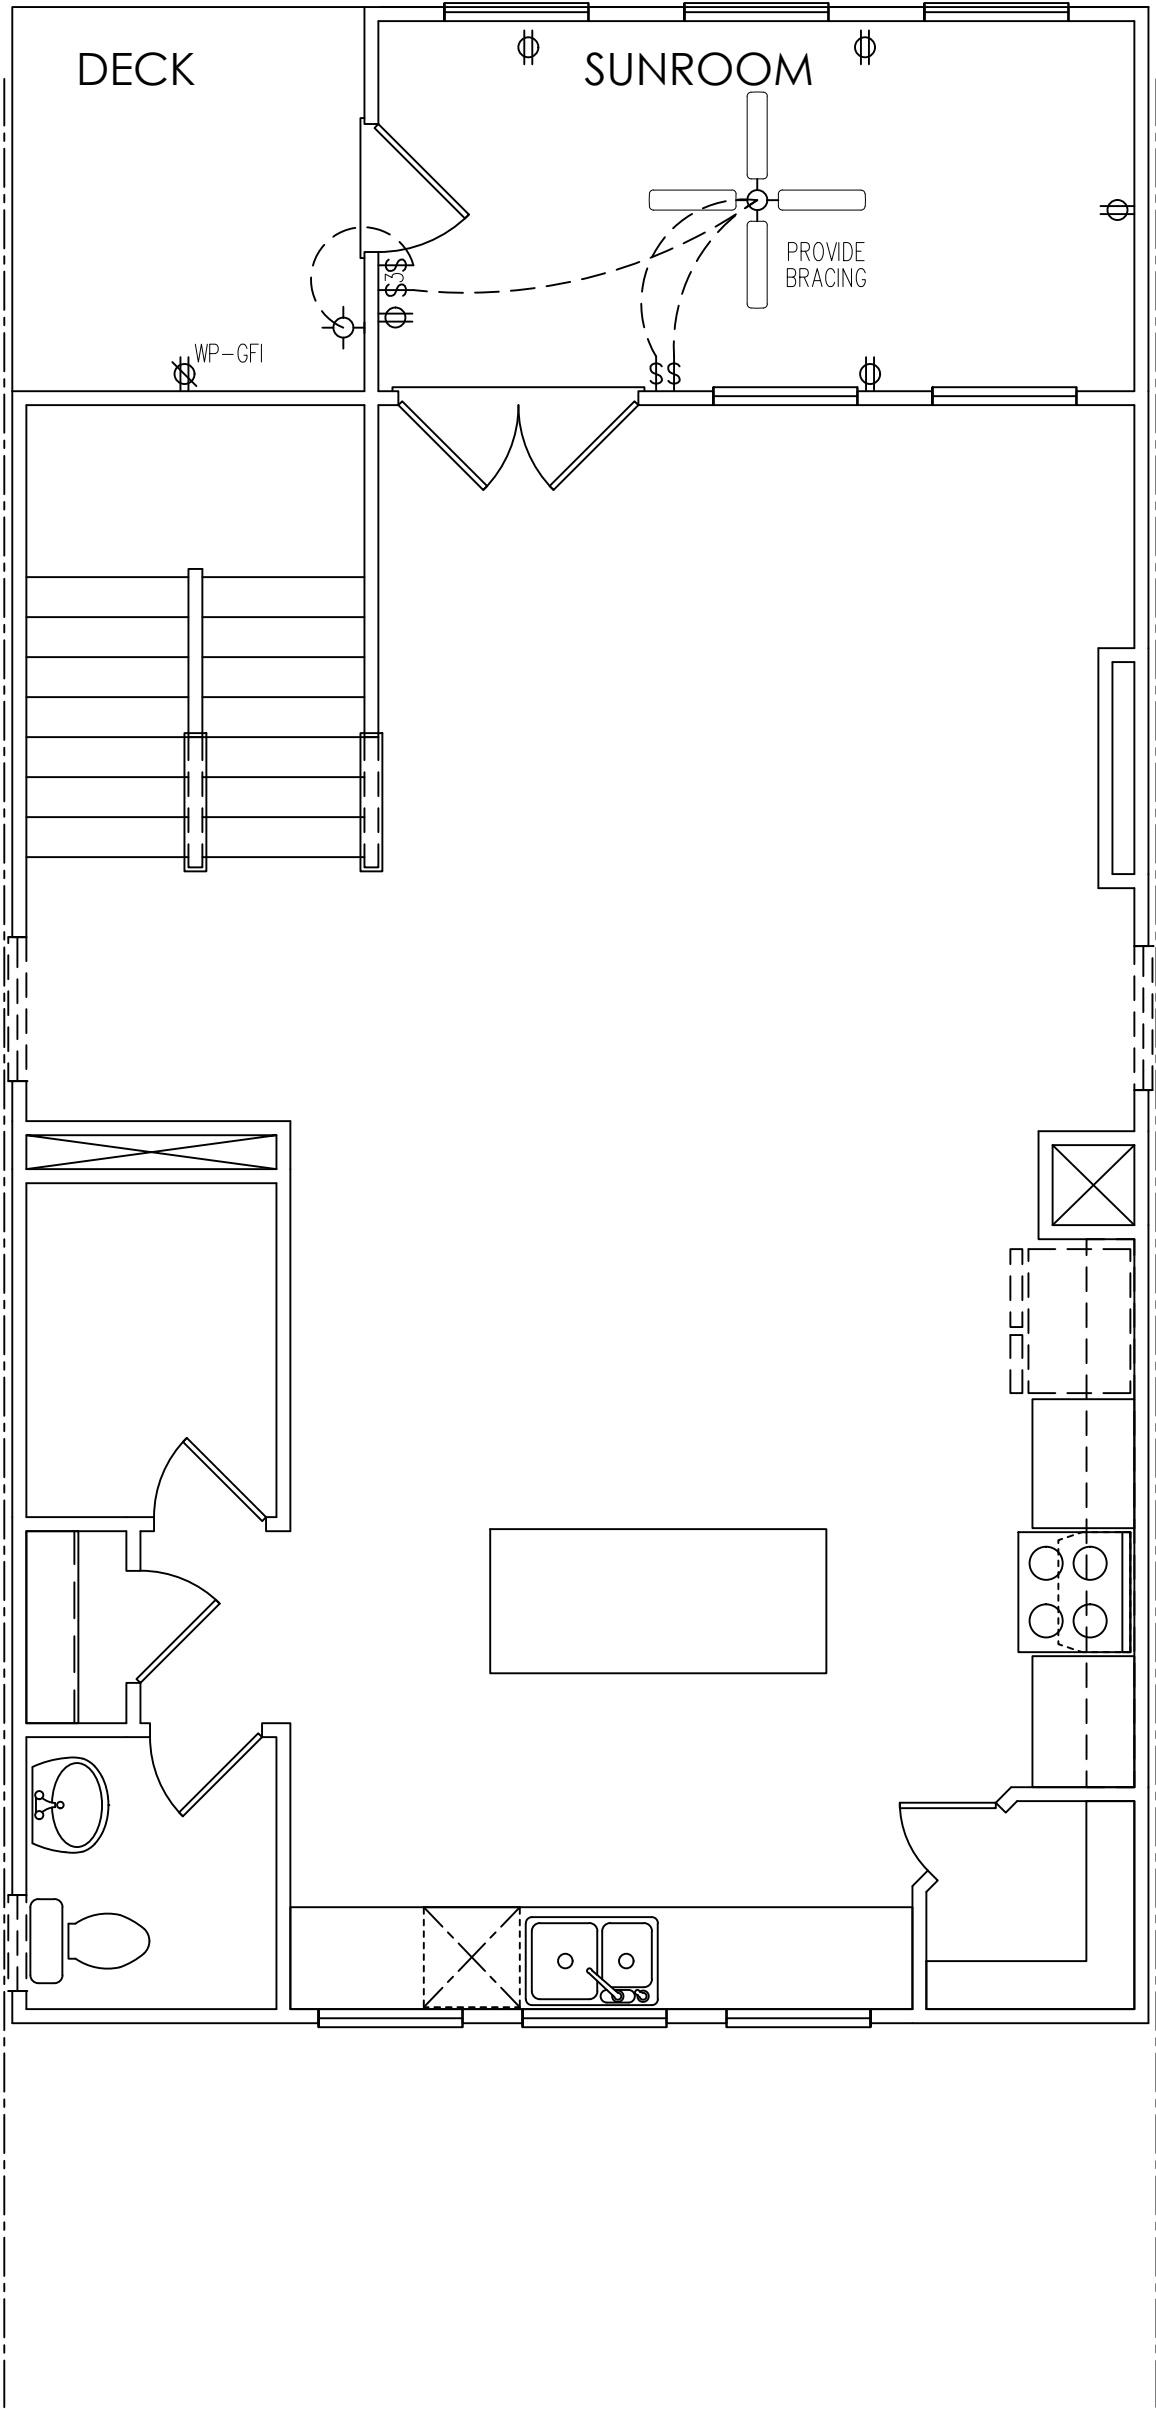

OPTIONAL SUNROOM

SCALE : 1/4" = 1'-0" - 24" x 36" SHEET
1/8" = 1'-0" - 11" X 17" SHEET


OPTIONAL FIREPLACE

SCALE : 1/4" = 1'-0" - 24" x 36" SHEET
1/8" = 1'-0" - 11" X 17" SHEET




OPTIONAL SUNROOM (REAR)

SCALE : 1/4" = 1'-0" - 24" x 36" SHEET
1/8" = 1'-0" - 11" X 17" SHEET

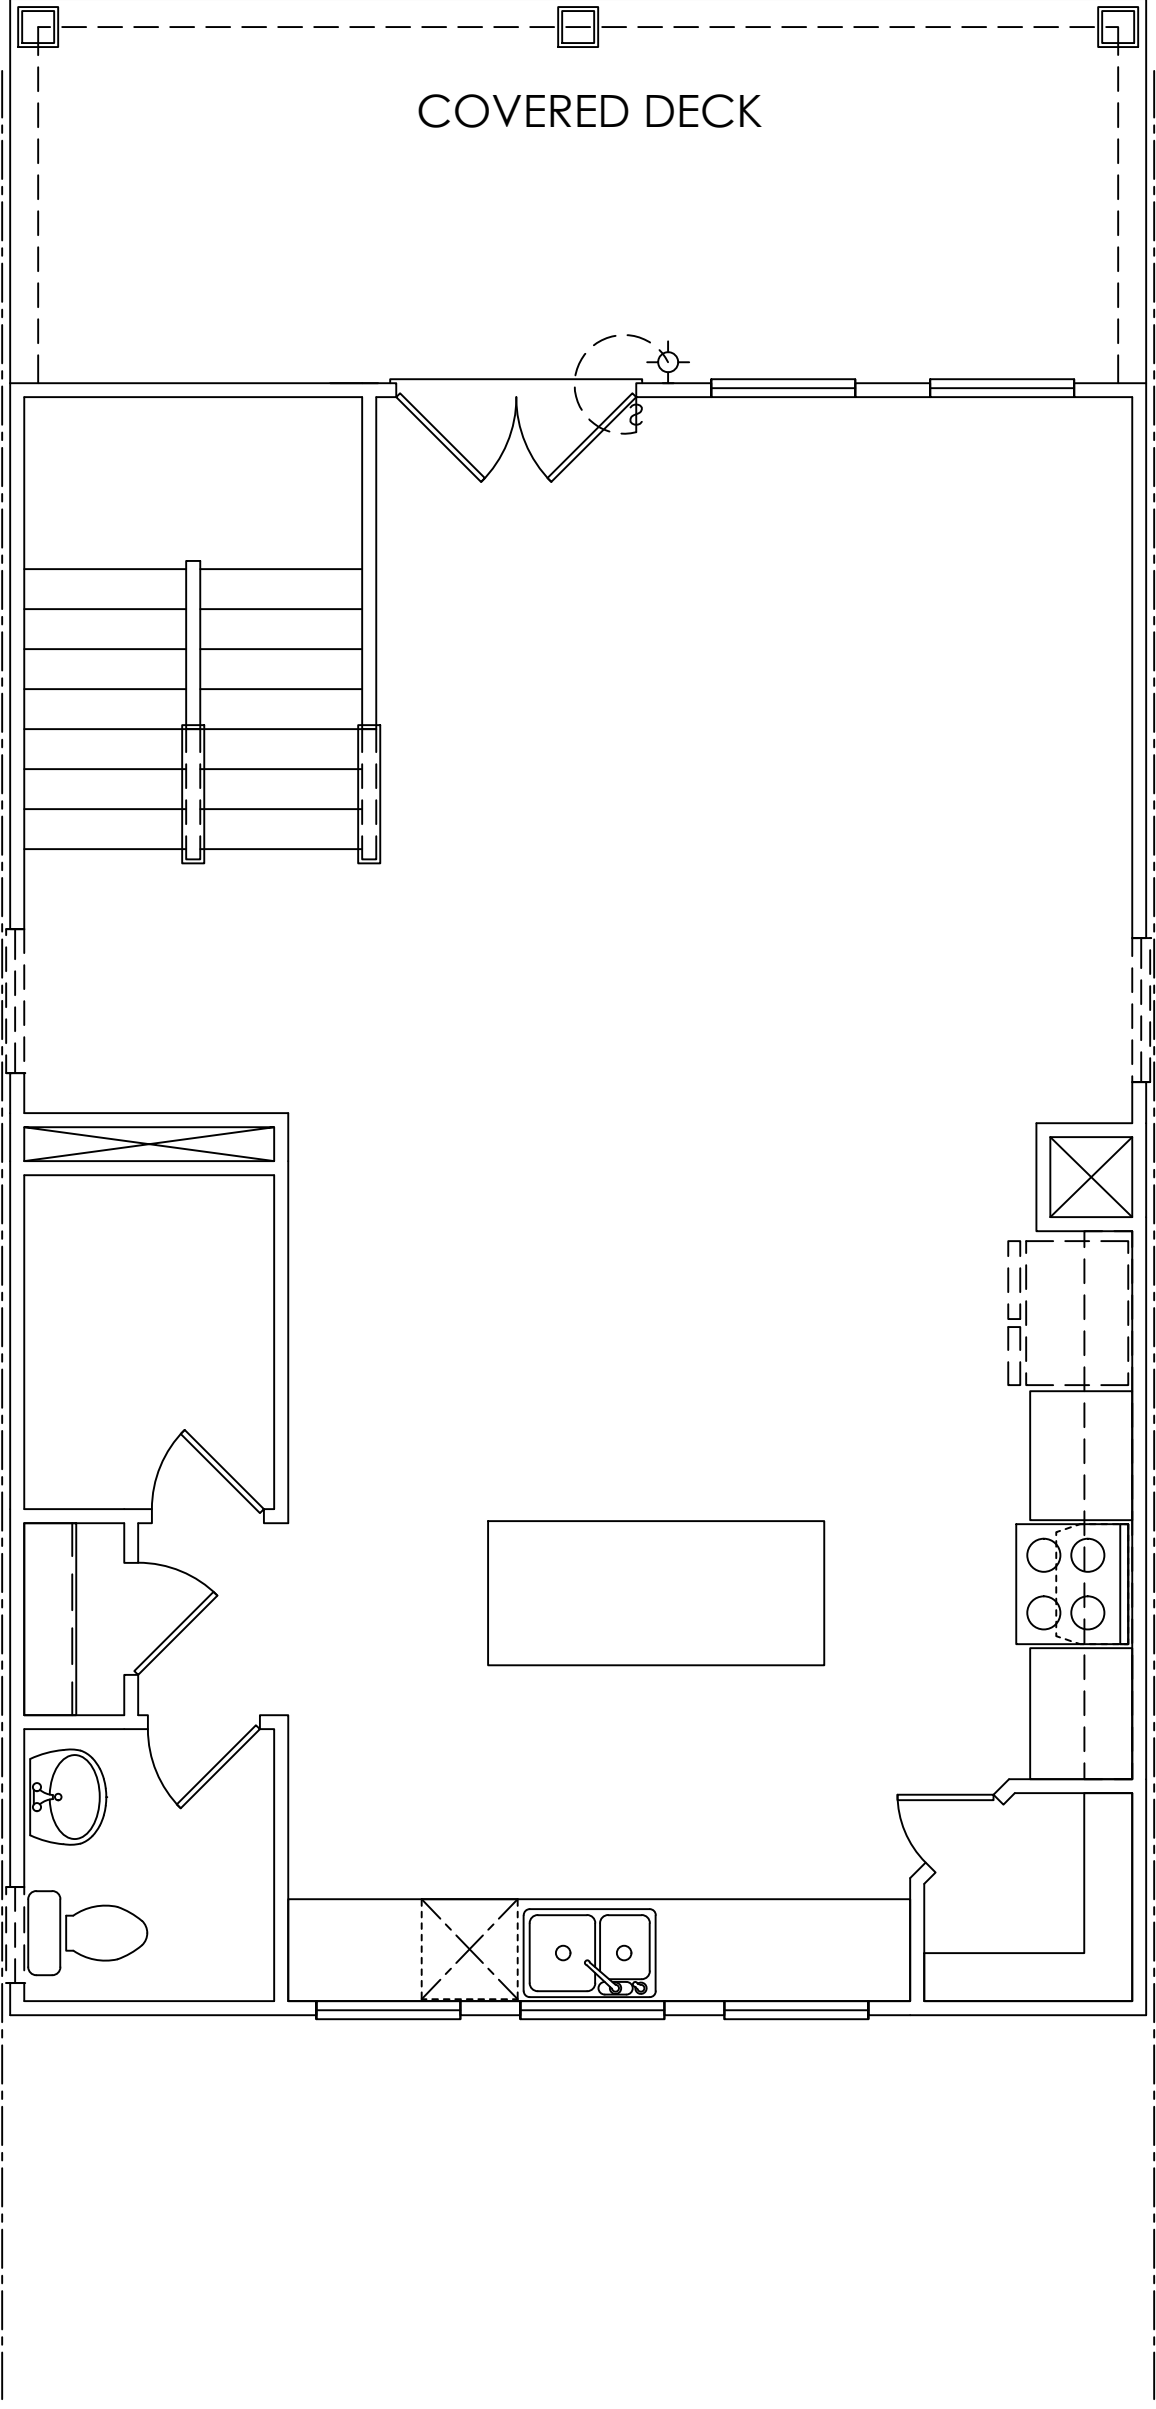


OPTIONAL FULL DECK

SCALE : 1/4" = 1'-0" - 24" x 36" SHEET
1/8" = 1'-0" - 11" X 17" SHEET

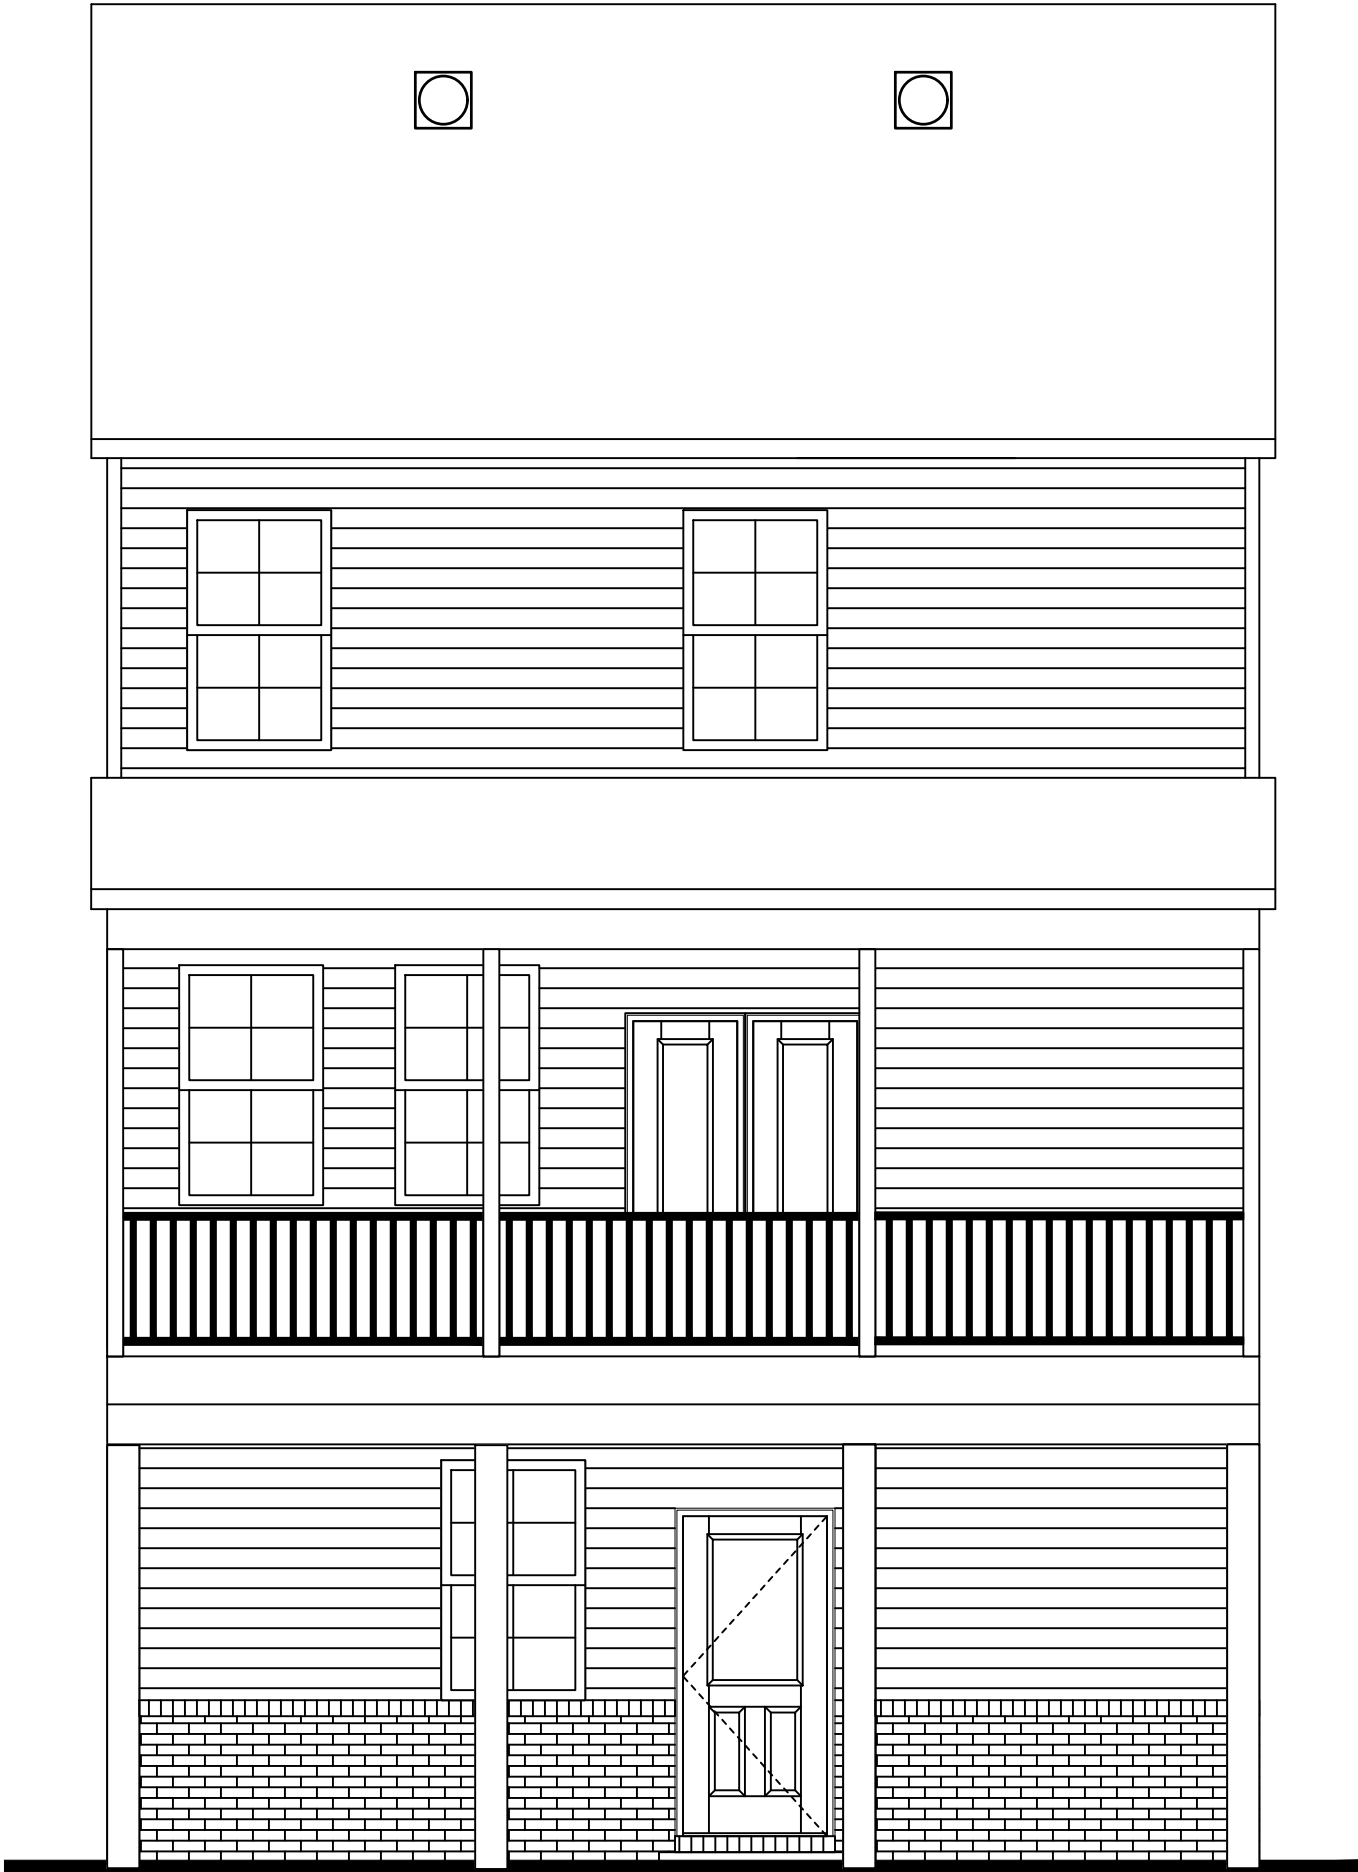

OPTIONAL FULL DECK (REAR)

SCALE : 1/4" = 1'-0" - 24" x 36" SHEET
1/8" = 1'-0" - 11" X 17" SHEET

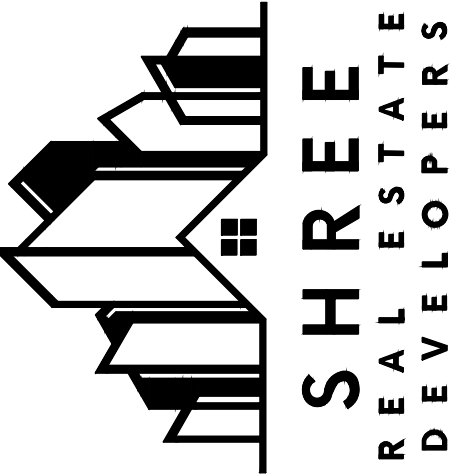

5400 LAUREL SPRINGS PKWY,
BLDG 700, STE 702
SUWANEE GA 30024
770-789-7044

REVISIONS

No	DESCRIPTION	No	DESCRIPTION
1		6	
2		7	
3		8	
4		9	
5		10	

RELEASE FOR
CONSTRUCTION

PROJECT:

FLOOR PLANS ELEC.
ASPEN

SHEET TITLE:

ELECTRICAL

DESIGNED BY :	PLAN NAME:
DRAWN BY :	SCALE:
CHECKED BY :	1/8"=1'-0"
REVIEWED BY :	PRODUCT TYPE:
RELEASE DATE:	SHEET:
	5.1.1